


STANDFORD RD.

LINDSAY RD

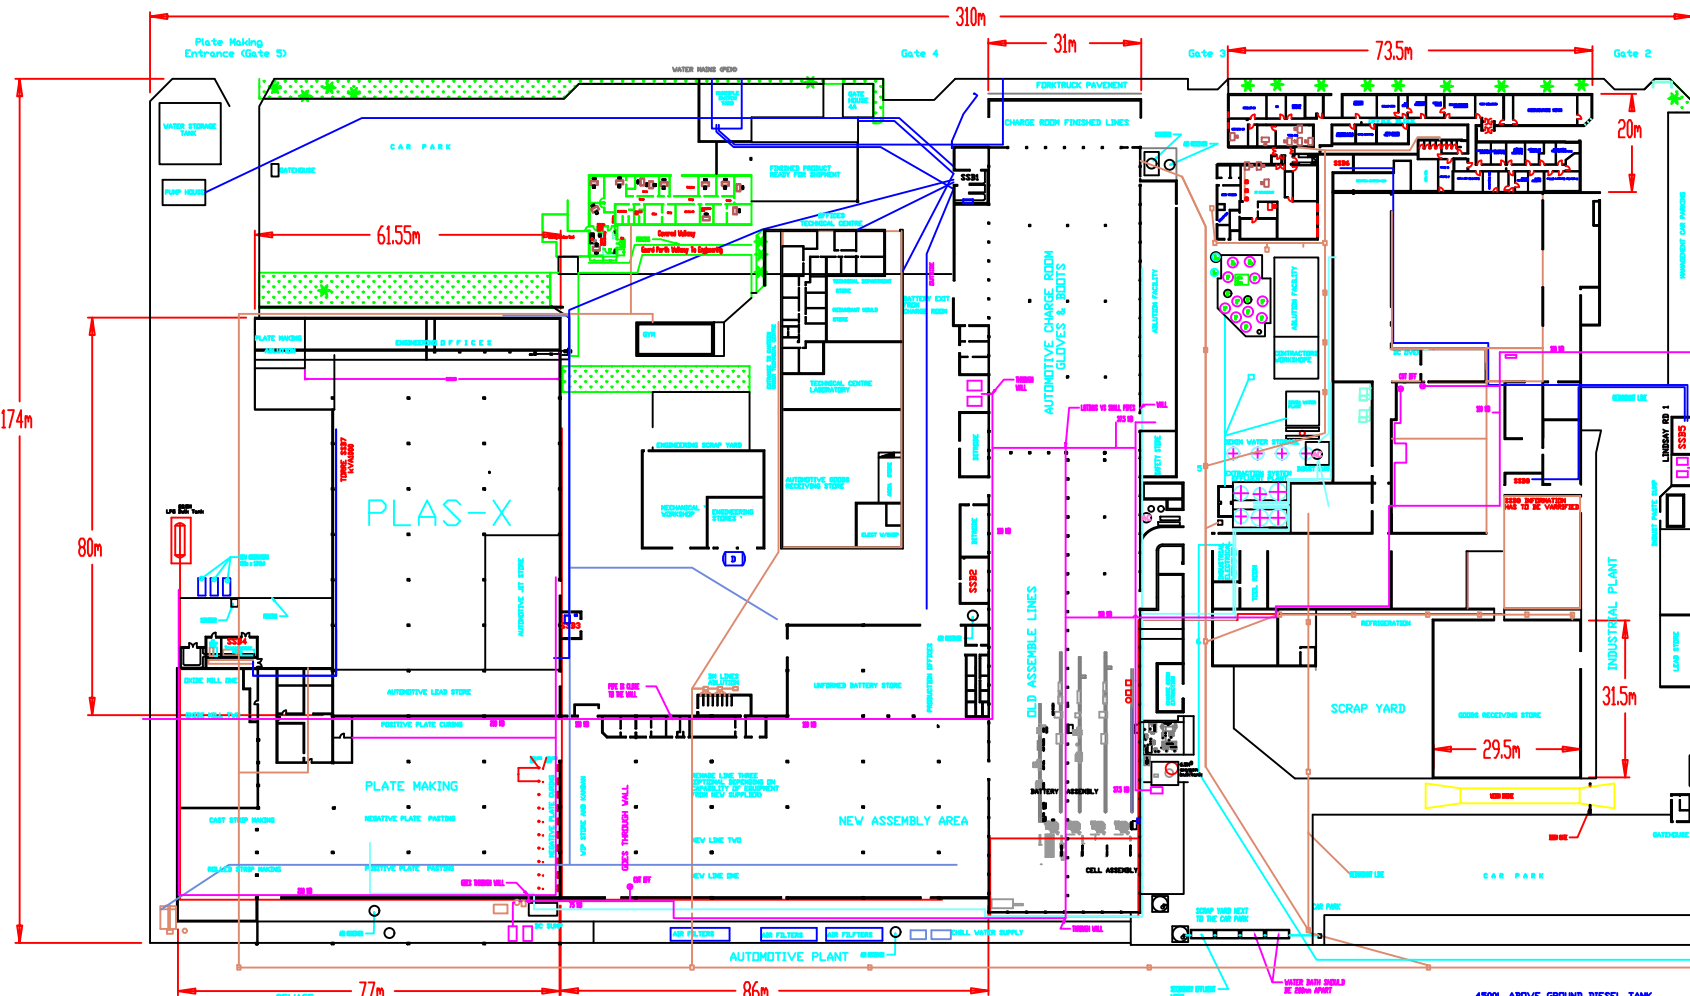

- SEWAGE
- STORM WATER
- EFFLUENT WATER
- ELECT. CABLES
- AIR LINE
- GAS MAINS
- EFFLUENT WATER DRAIN

- 4500L DIESEL TANK
- 10000L CHILLED ACID STORAGE TANK
- 30000L CONC ACID STORAGE TANK
- 10000L CHILLED WATER TOWER

Auto X (Pty) Ltd

Company Registration No: 2004/0000000/07
Stanford Road/Leve Road/Port Elizabeth/South Africa

THIS DRAWING IS
COPYRIGHT AND MAY
NOT BE USED OR
REPRODUCED WITHOUT
THE WRITTEN
PERMISSION OF THIS
COMPANY

REV.	DATE	MODIFICATION
04		
03		
02		
01		

TITLE: SITE PLAN
WILLARD BATTERIES

Drawn: V. MDA
Date: 01-01-2006
Scale: 1:500
CHK'd: [Signature]
Appr: [Signature]

Proj. No: WE-0027-001
Rev: 00
Sheet of 1 Sheets