

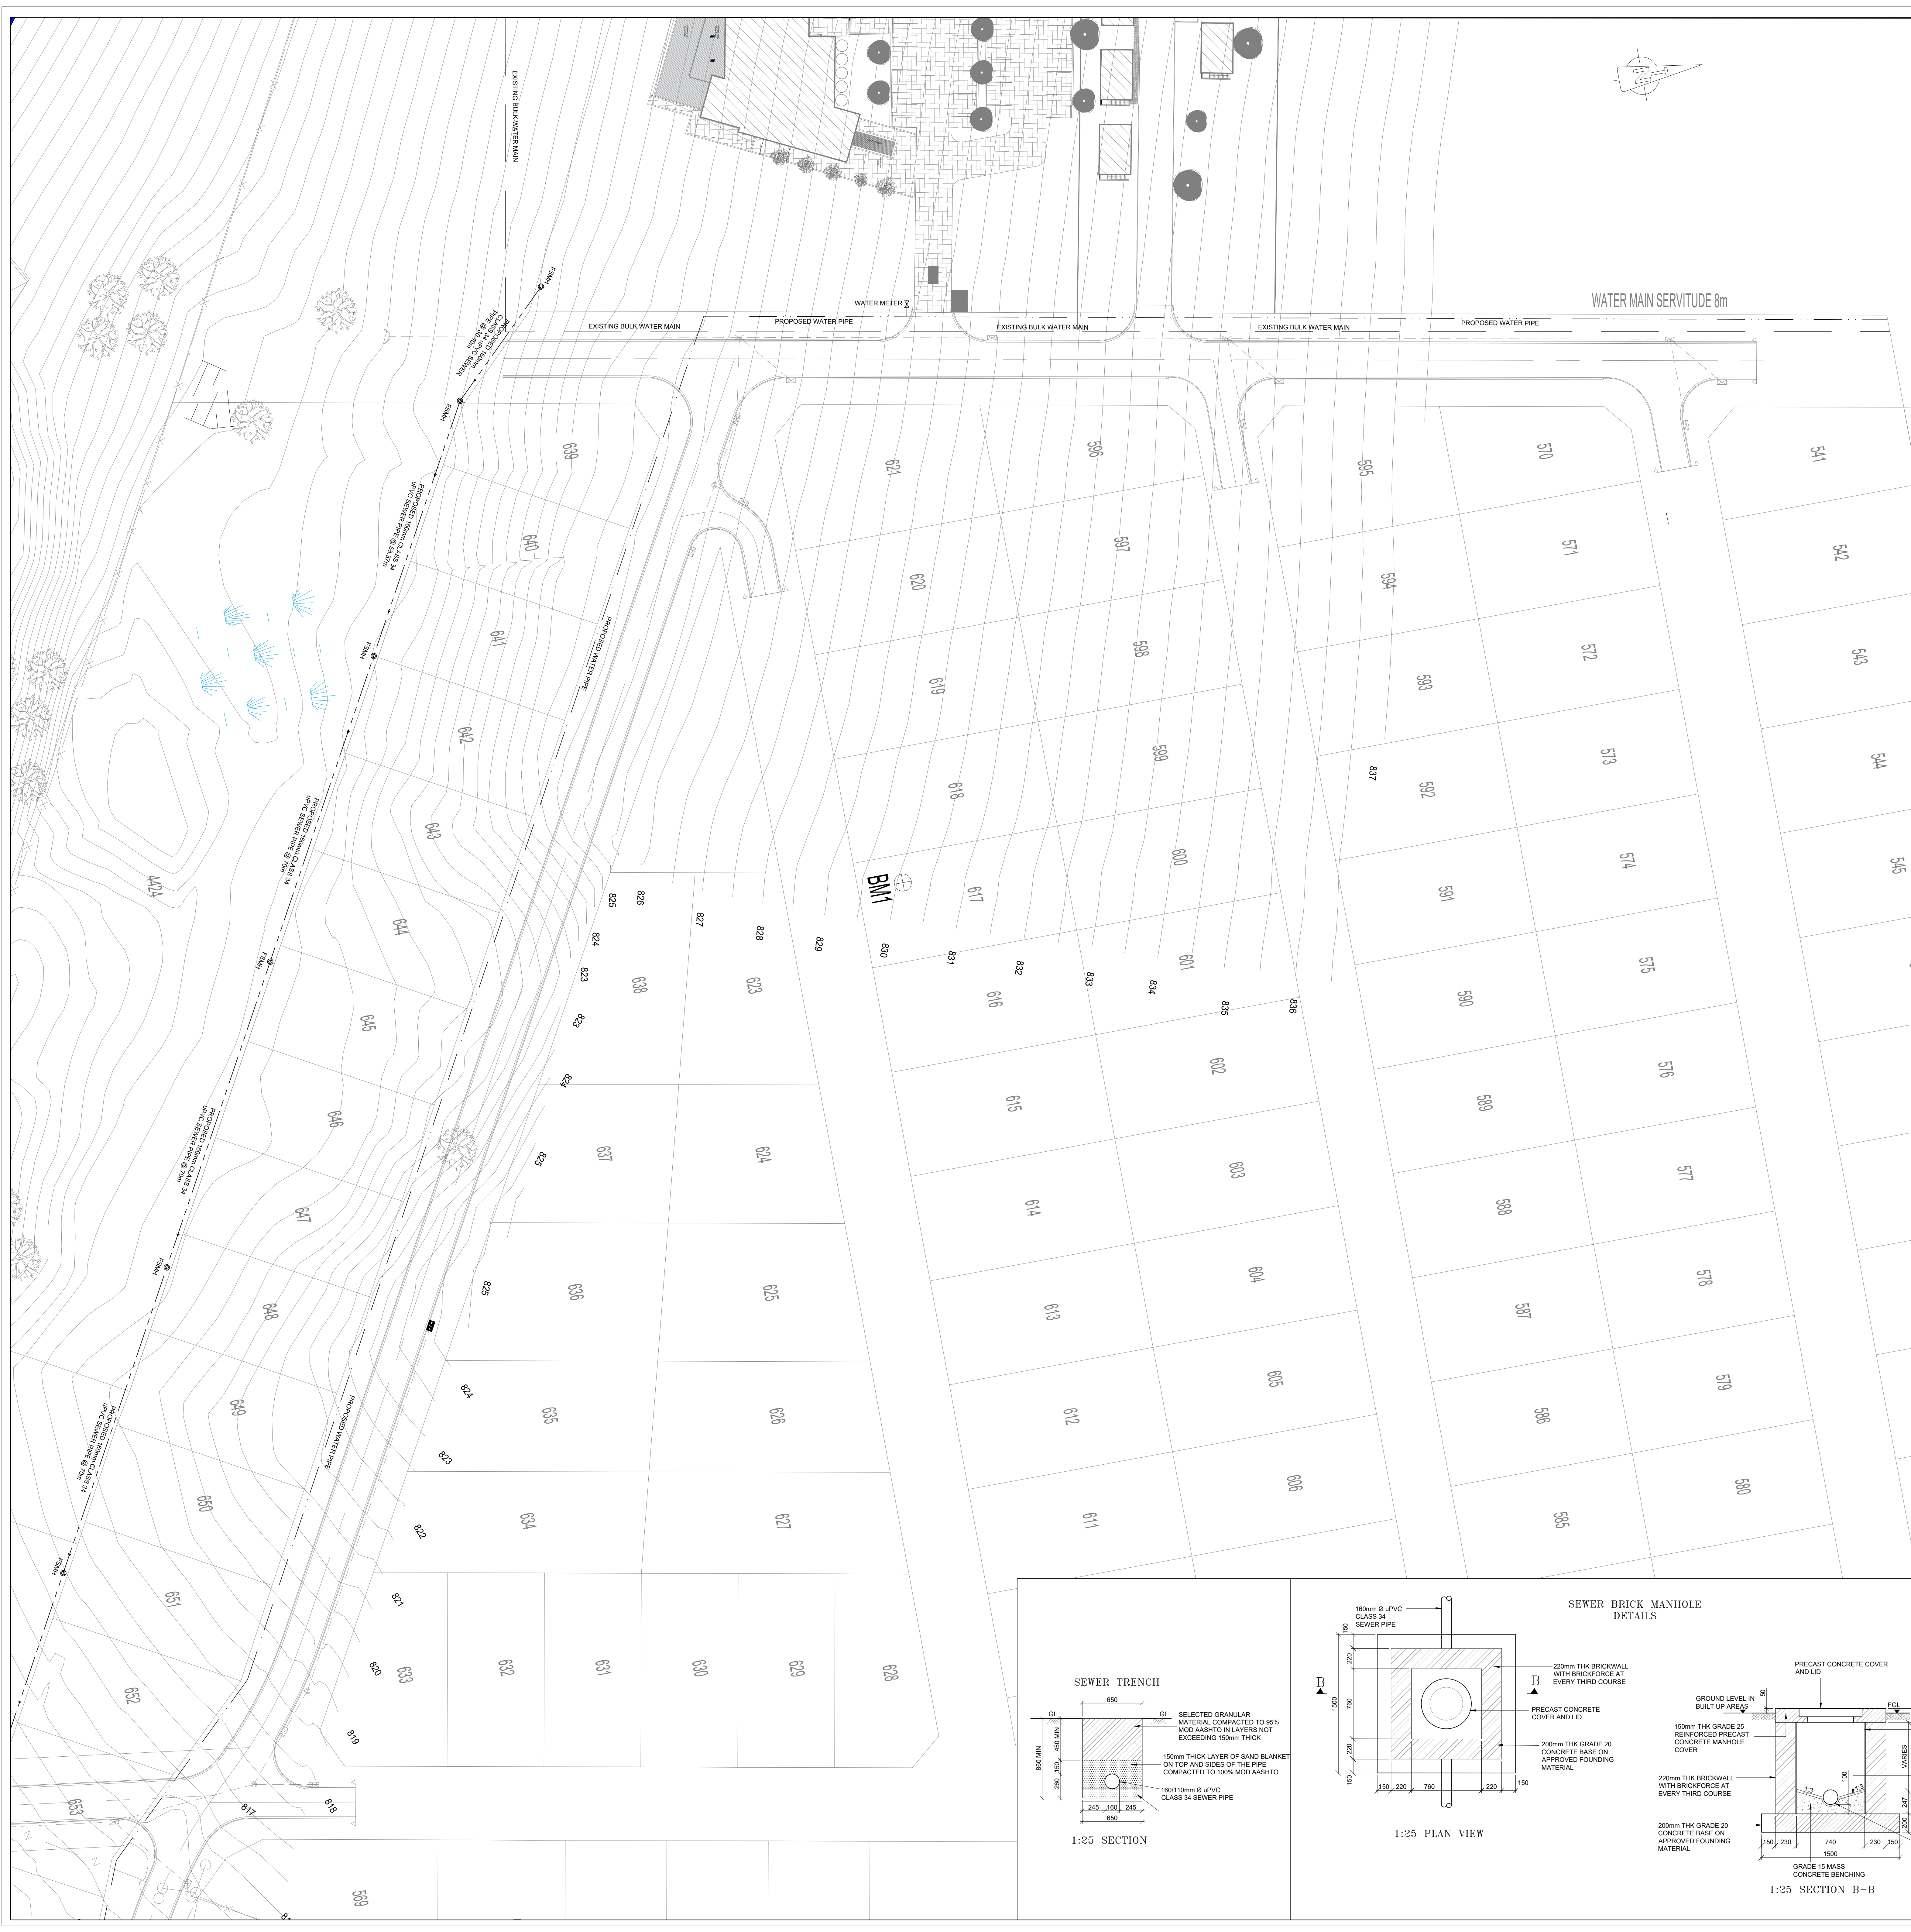
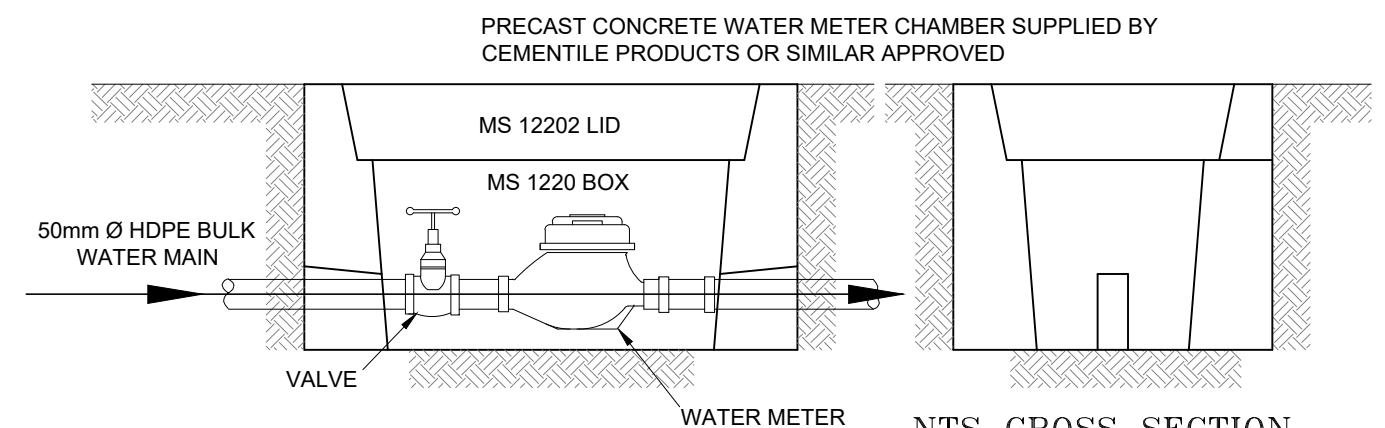
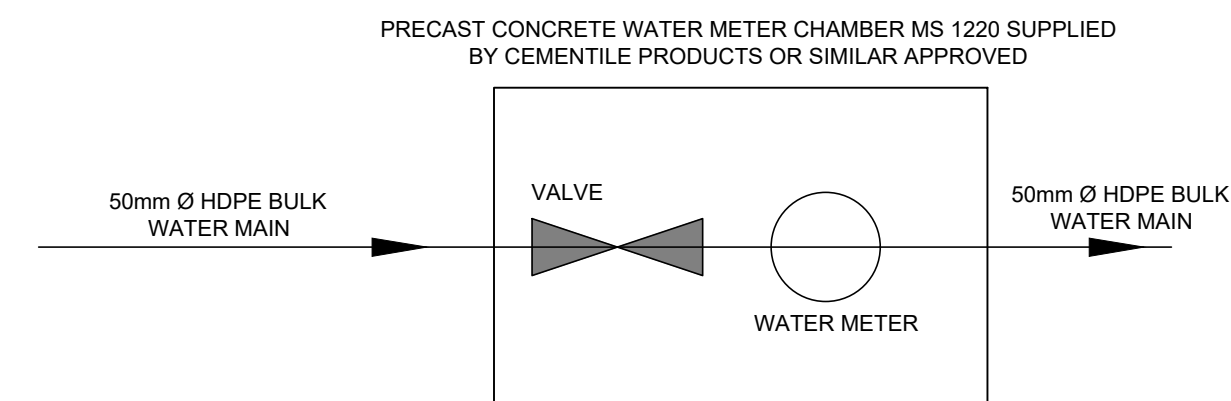


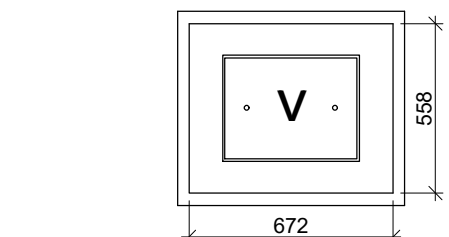


DETAILS OF ABOVE GROUND FIRE HYDRANTS
SCALE : NTS

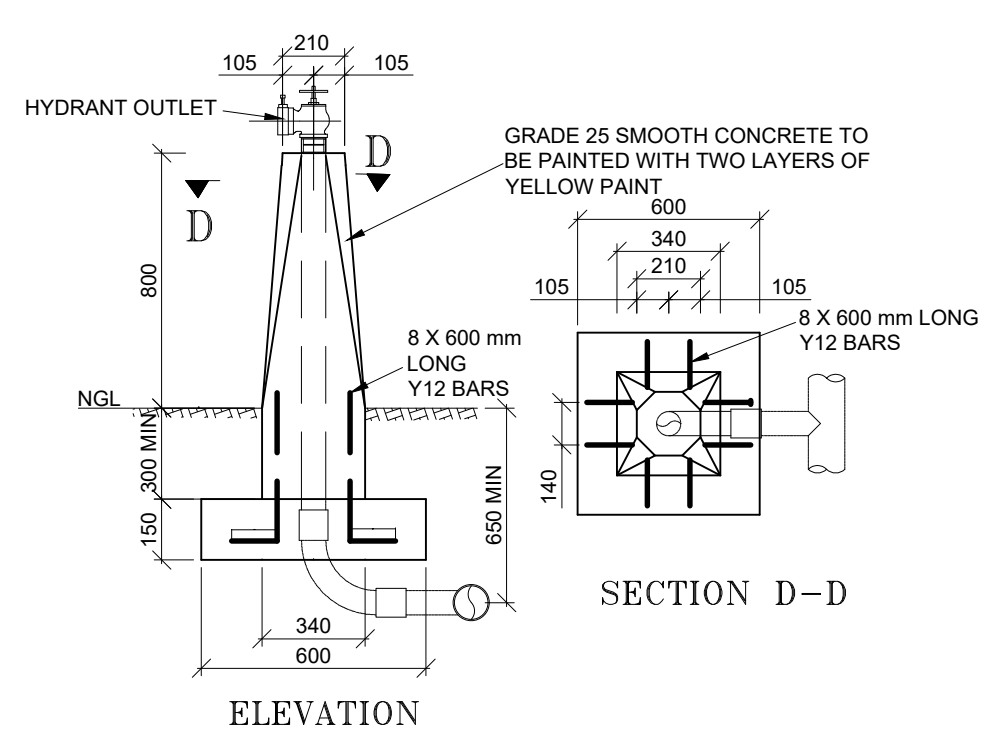

NTS LONG SECTION

TYPICAL THRUST BLOCK DETAILS
SCALE : NTS

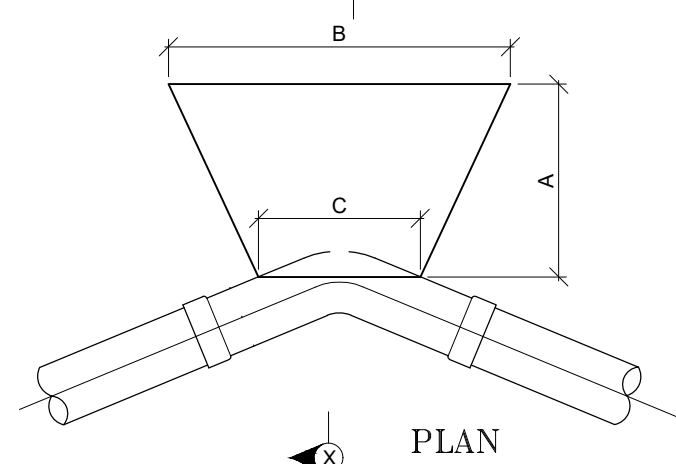



ANGLE		63 Ø	110 Ø
11 1/4	A	250	300
	B	125	200
	C	75	100
	D	250	300
22 1/2	A	250	300
	B	125	200
	C	75	100
	D	250	300
45	A	250	300
	B	200	250
	C	105	150
	D	250	300
90	A	250	300
	B	300	400
	C	150	250
	D	250	300

- NOTES:
1. THESE DIMENSIONS AND THE FORM OF THE BLOCK ARE INTENDED AS A GUIDE ONLY. THE FINAL SHAPE IS TO BE DETERMINED ON SITE
 2. WHERE POSSIBLE THE BLOCK IS TO BE CAST AGAINST UNDISTURBED INST. MATERIAL
 3. THE COUPLING MUST REMAIN FLEXIBLE AND REMOVABLE.


NOTE THAT THIS TRUST BLOCK IS APPLICABLE TO ALL BENDS AND TEE FUNCTIONS

SECTION X - X


TYPICAL SEWER CONCRETE
RING MANHOLE DETAIL

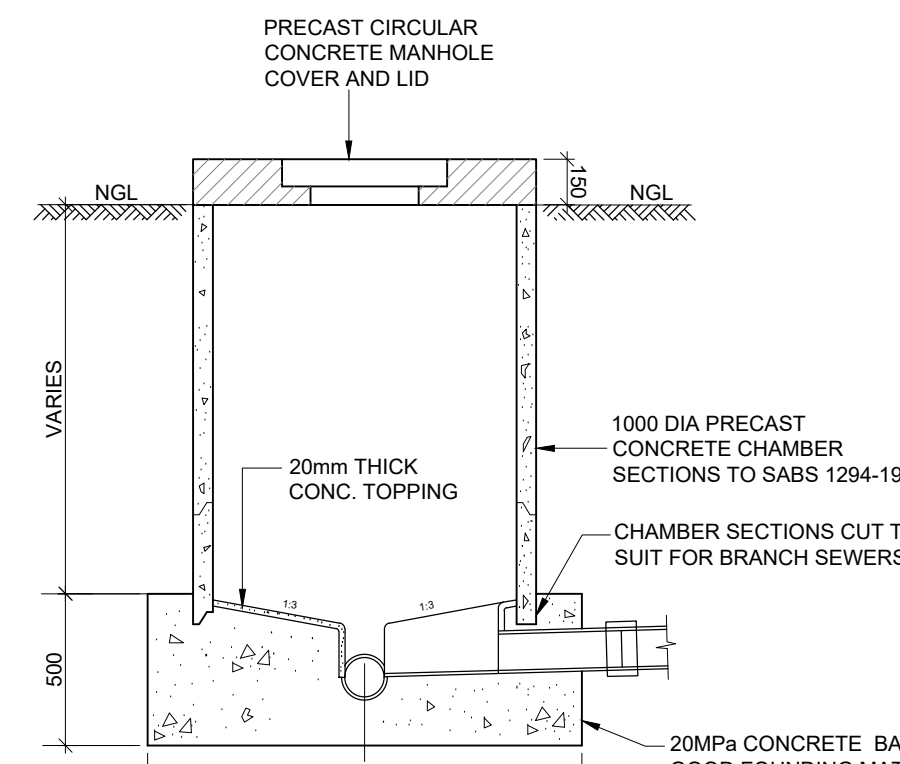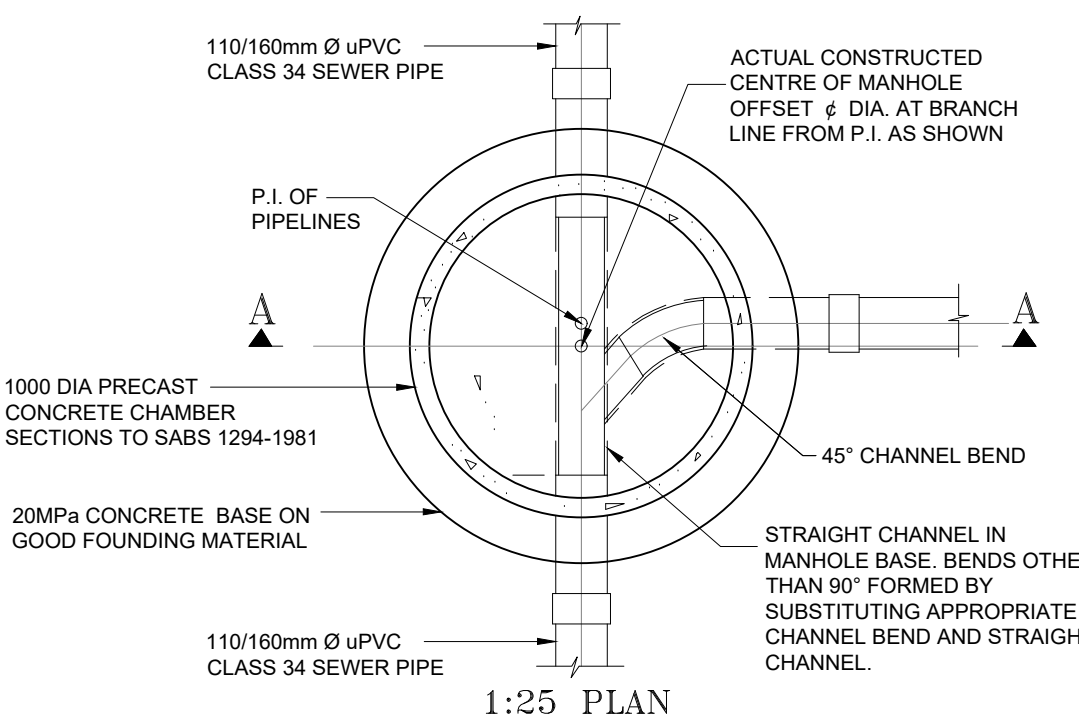

SEWER TRENCH

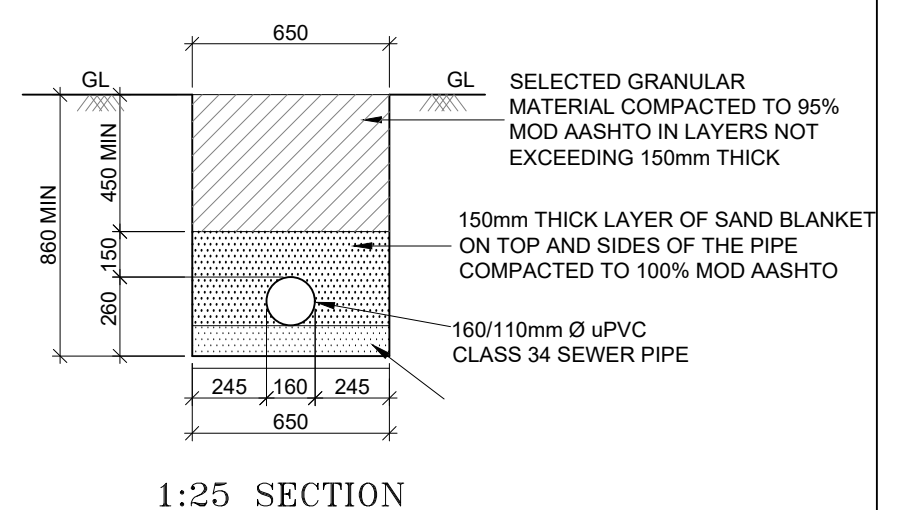

SEWER BRICK MANHOLE
DETAILS

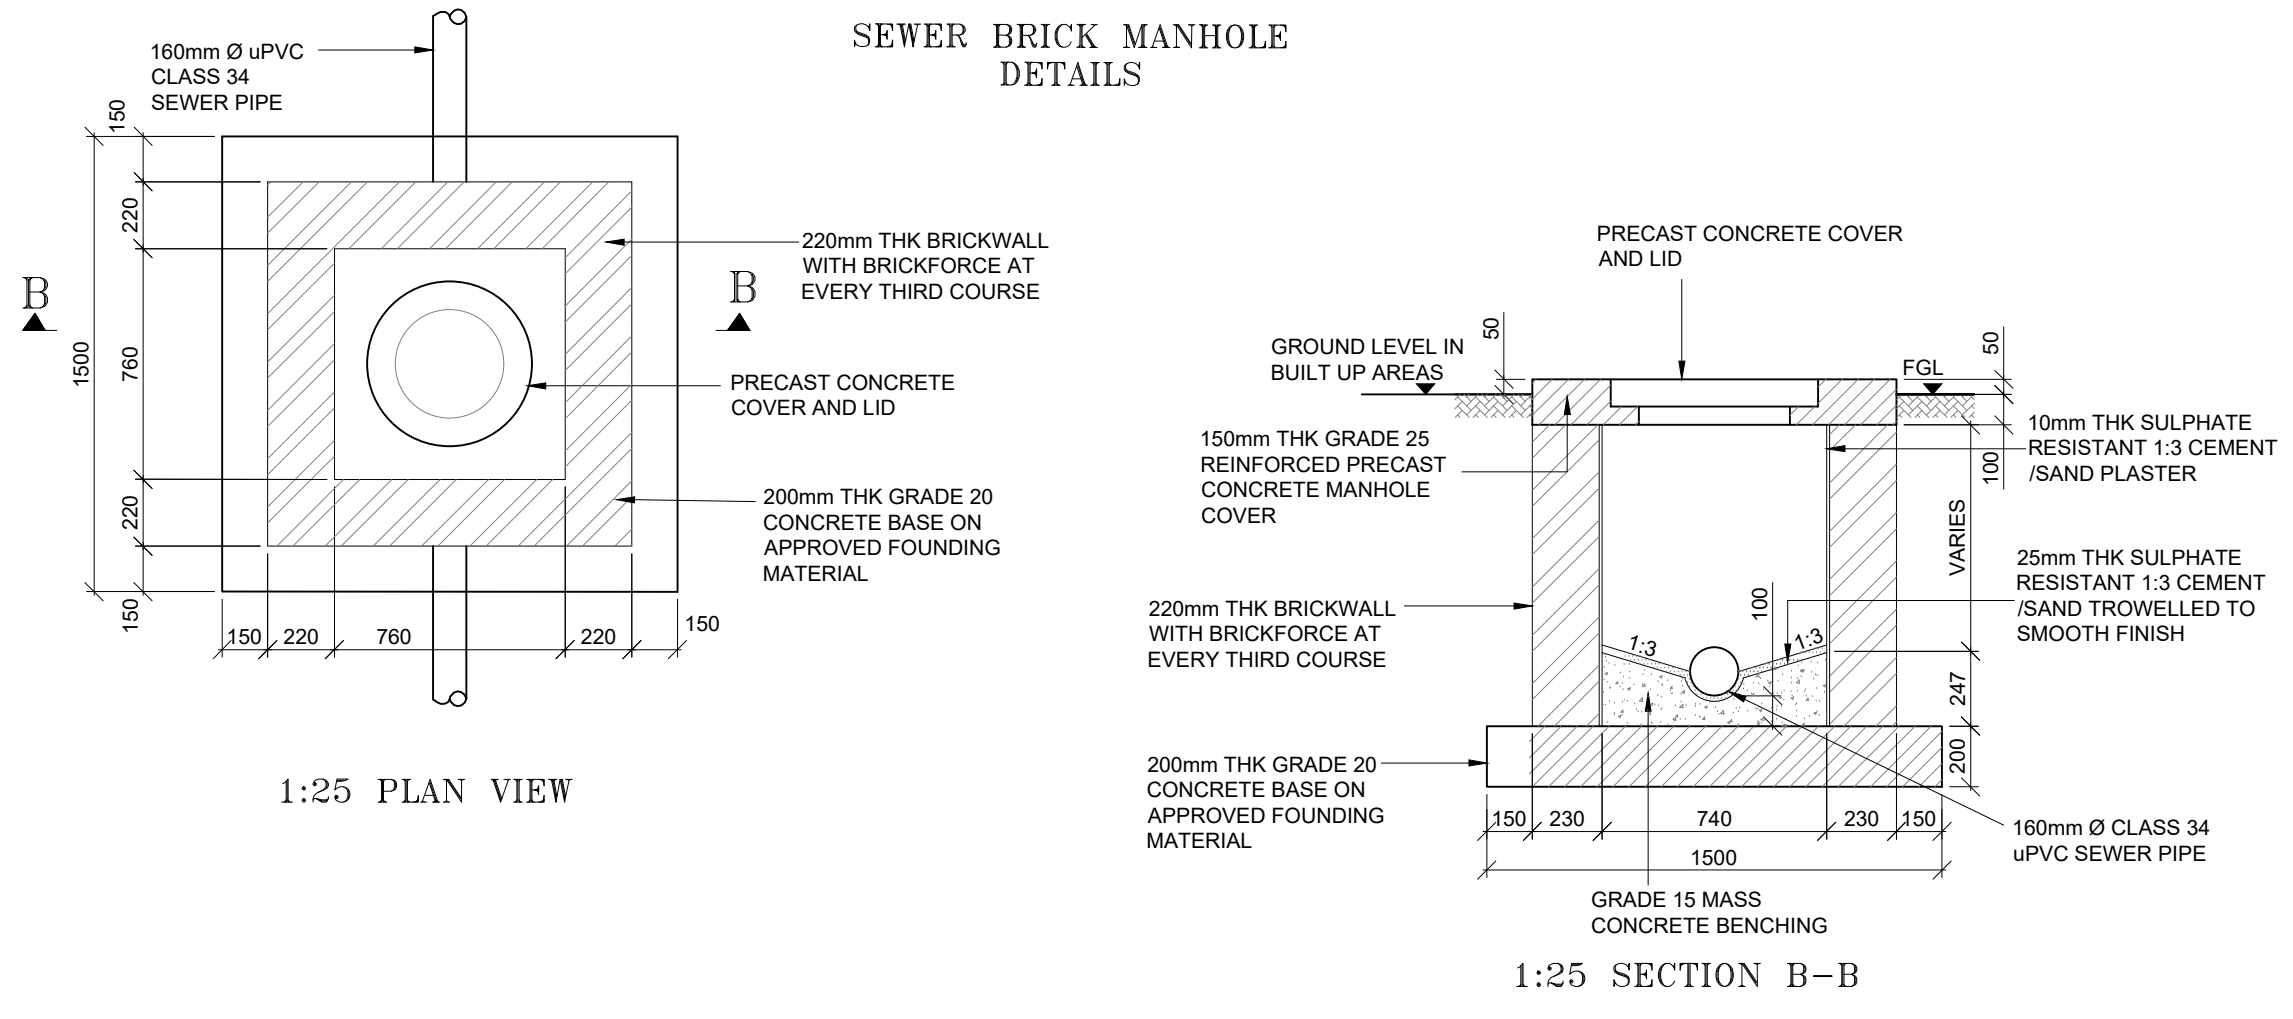

FOR INFORMATION

REV.	DATE	DETAILS	Chd	Appd
A	07-05-2026	INFORMATION		



**NONXUBA CONSULTING
ENGINEERING SERVICES**
Civil, Structural & Project Management

No. 20 LATIMER STREET
BEREA
EAST LONDON 5201

P.O. BOX 785
EAST LONDON, 5200
TEL: (043) 700 7700
FAX: (043) 742 2891

Email : nces_ei@nonxubaconsulting.co.za

PROJECT
**MBHASHE MUNICIPALITY
RECREATION CENTRE**

DESCRIPTION
**WATER AND SEWER
LAYOUT AND DETAILS**
Sheet 1 of 2

Drawn NJ	Checked MN	Designed NJ
-------------	---------------	----------------

Scale 1:500 @ A0	Date APRIL 2026
---------------------	--------------------

Project No EL039-2026	Drg. No 102	Rev A
---------------------------------	-----------------------	-----------------