

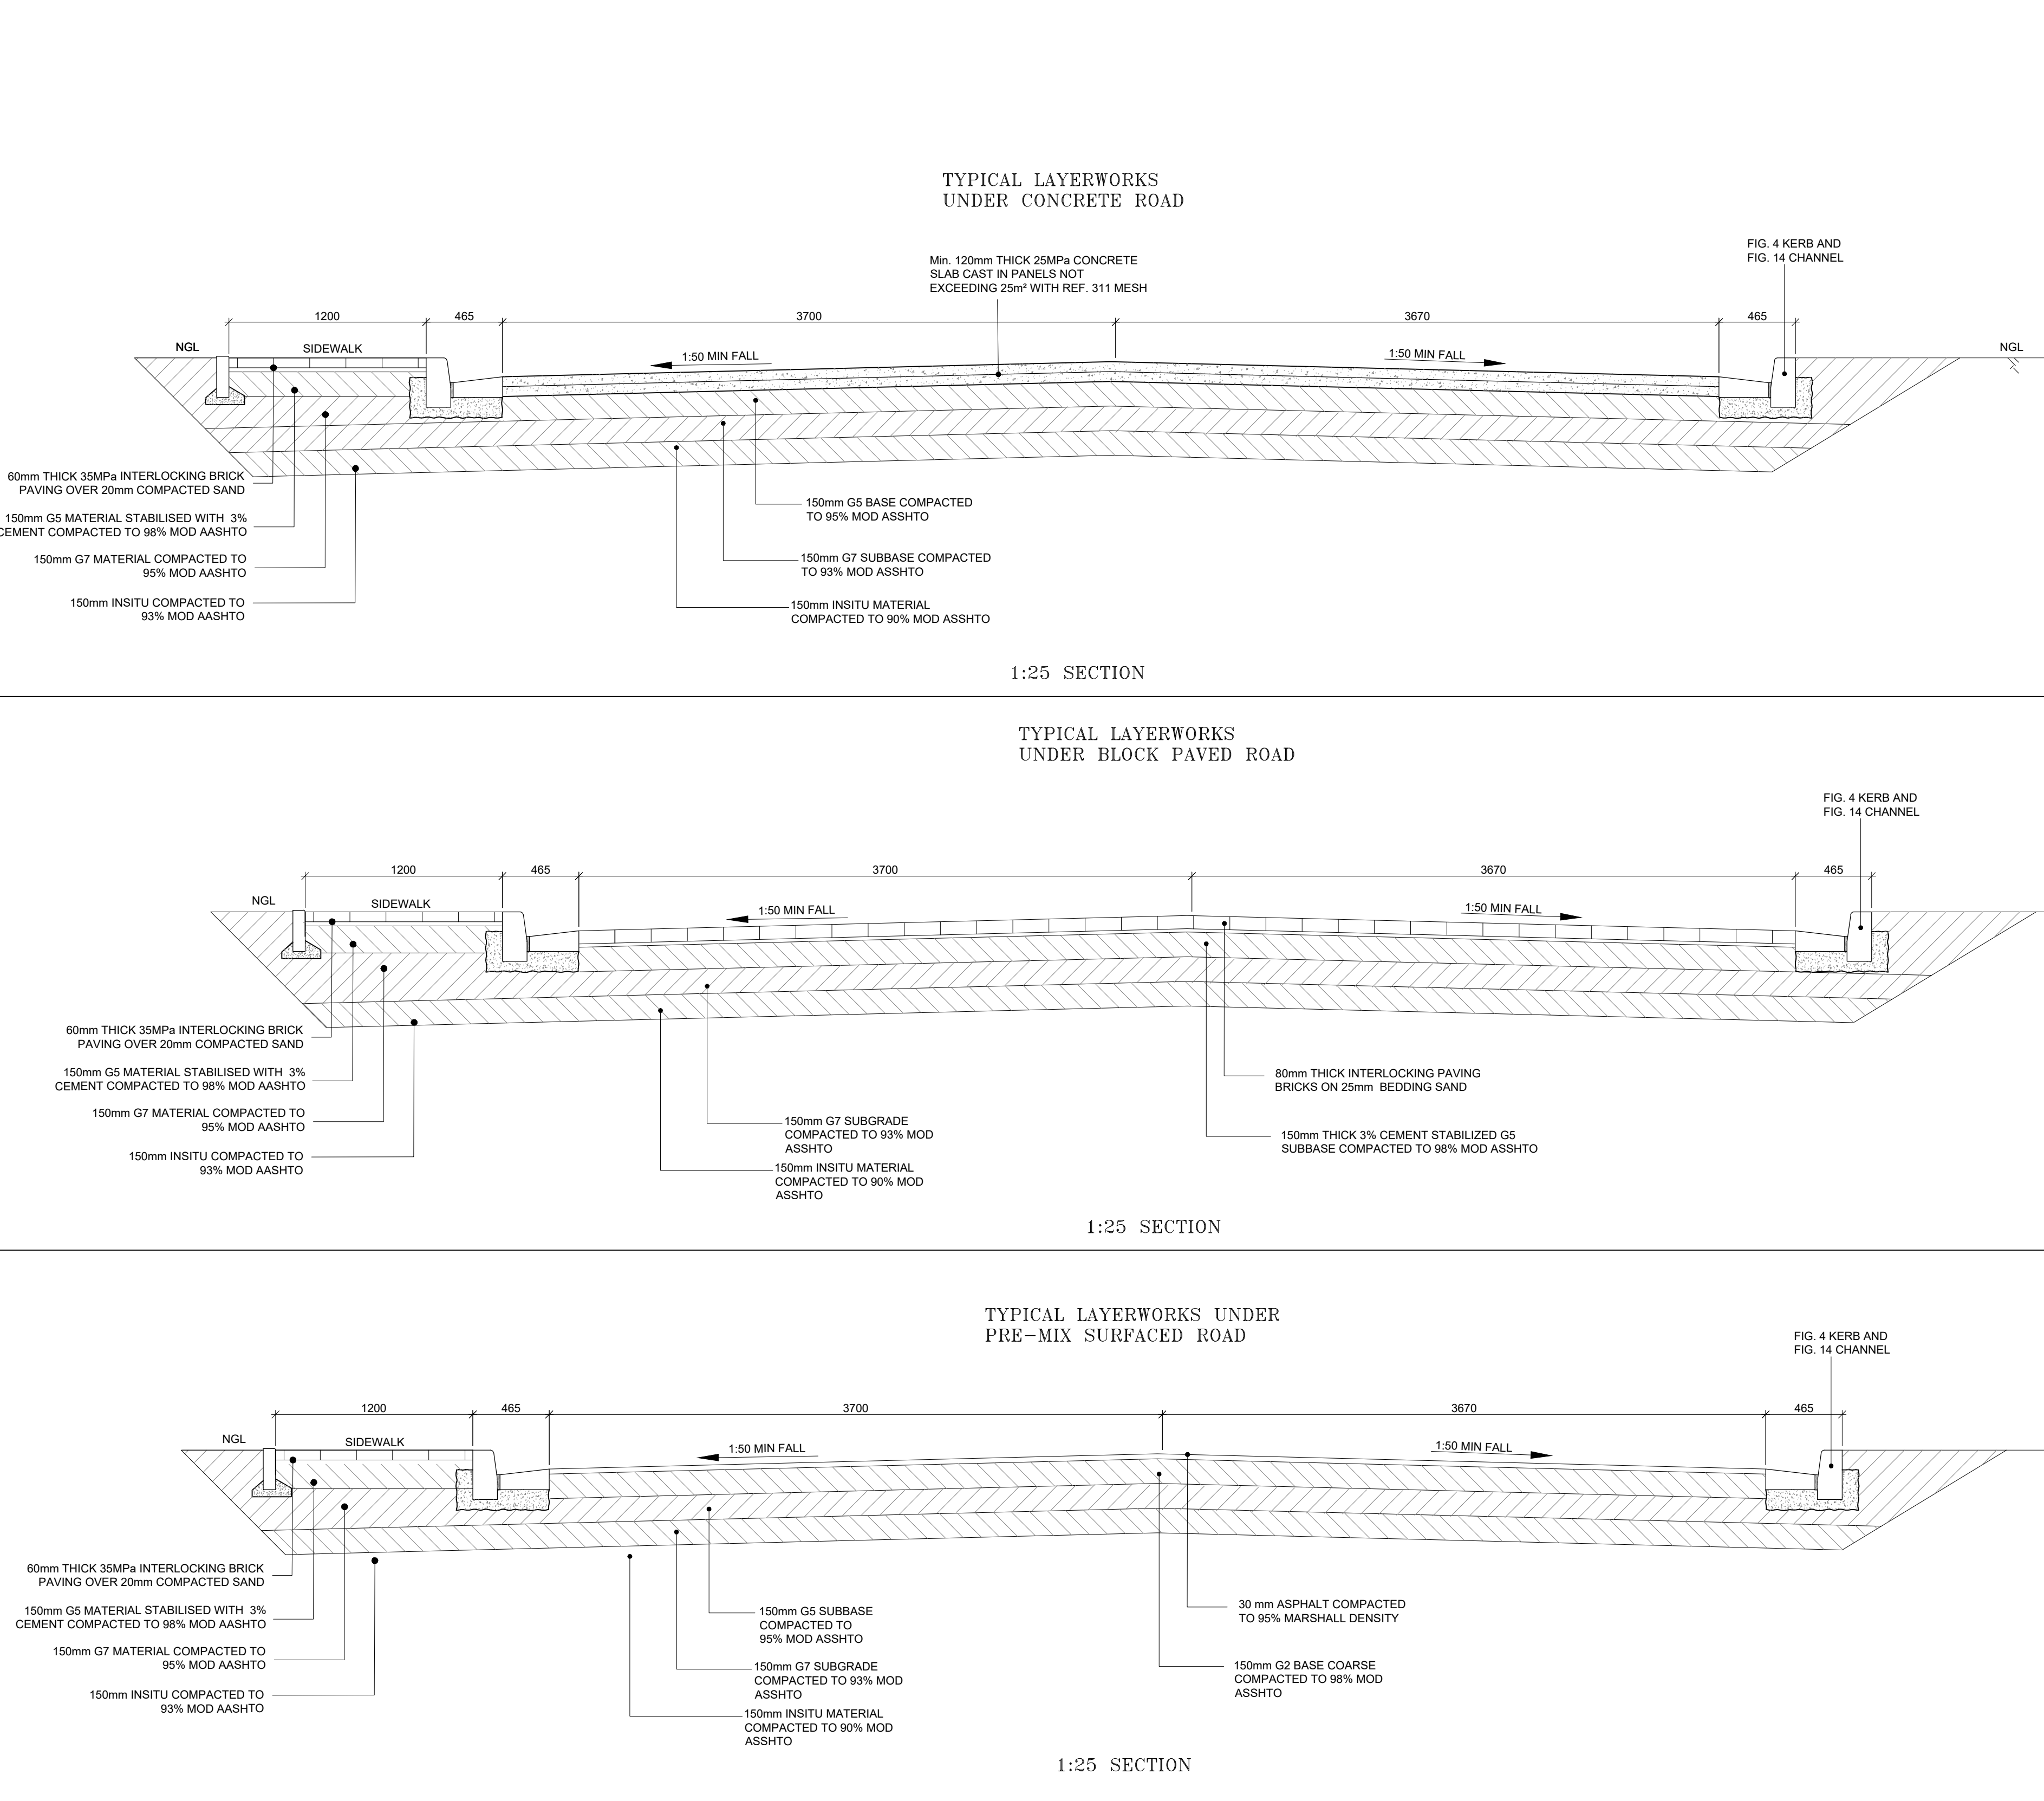
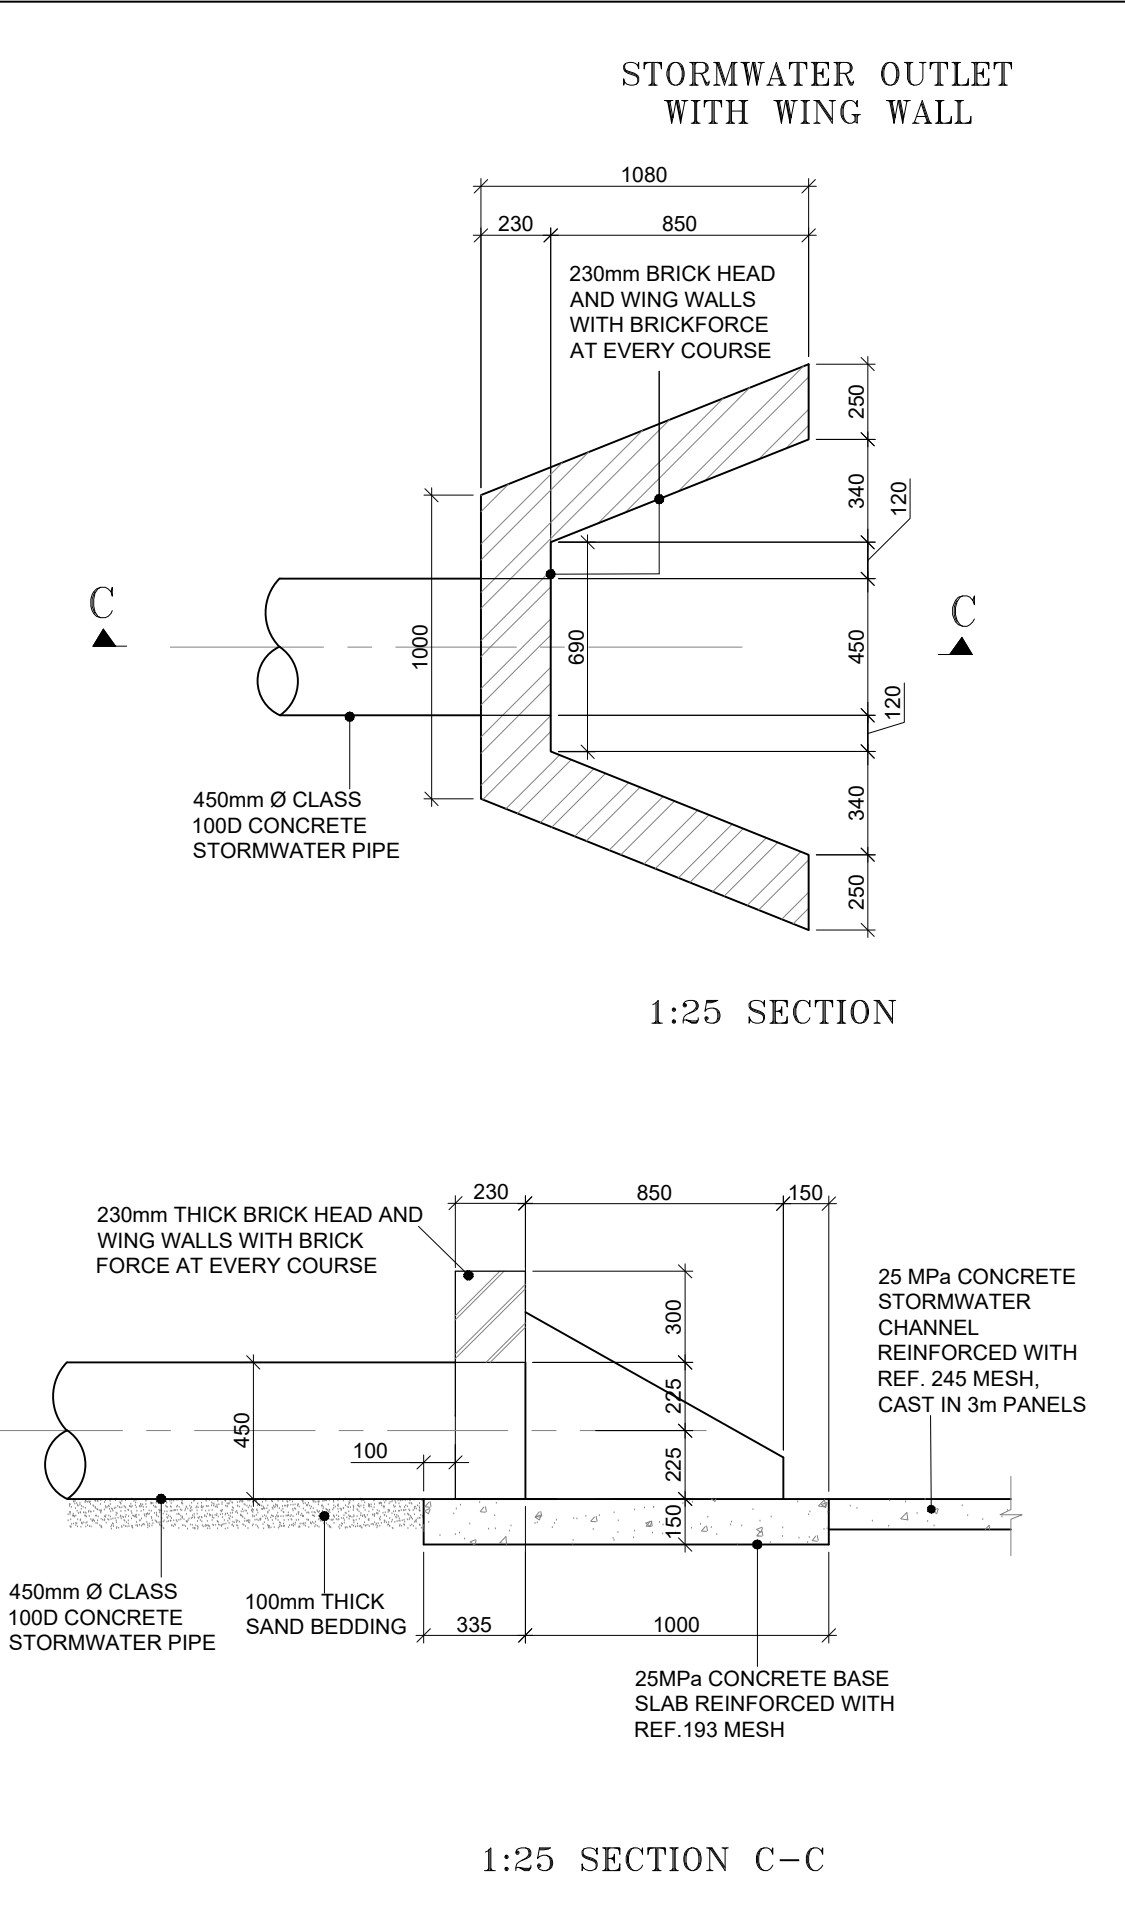
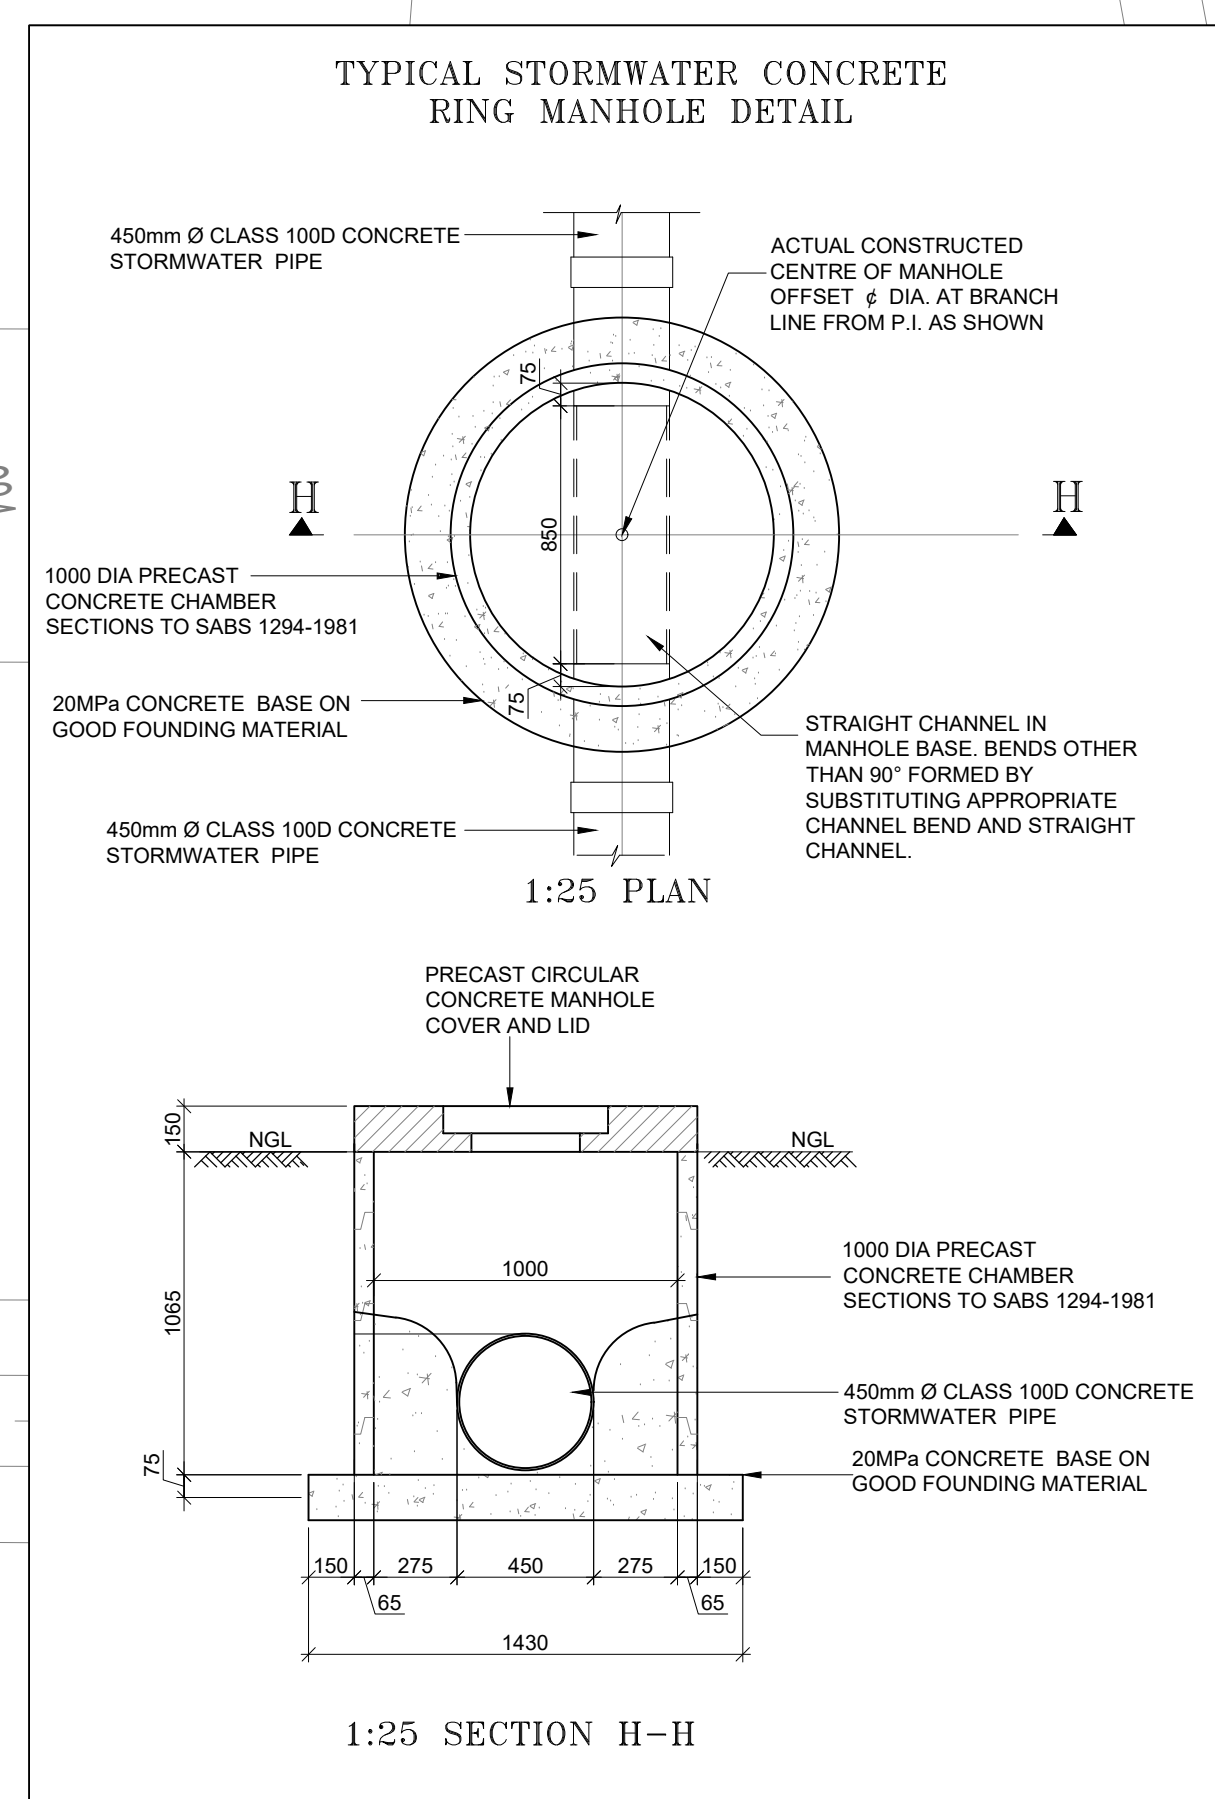
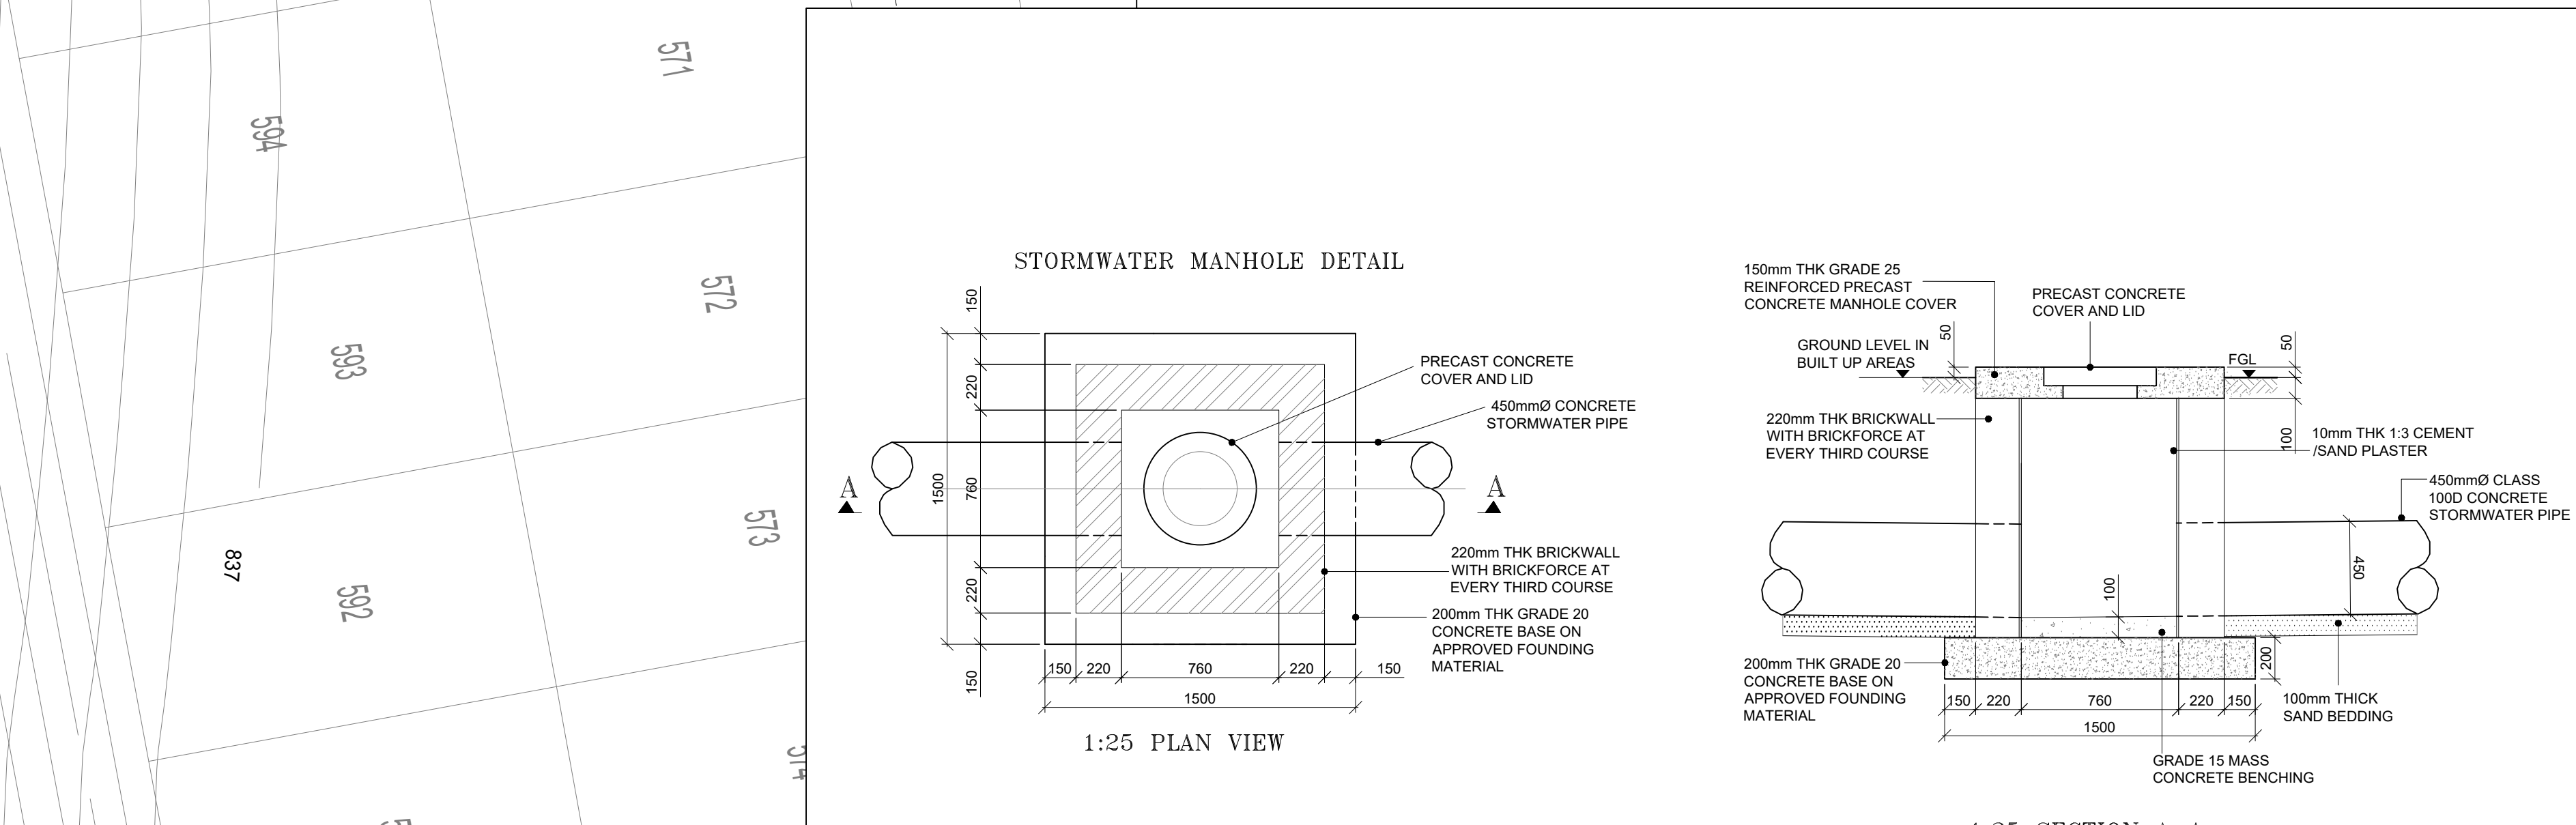
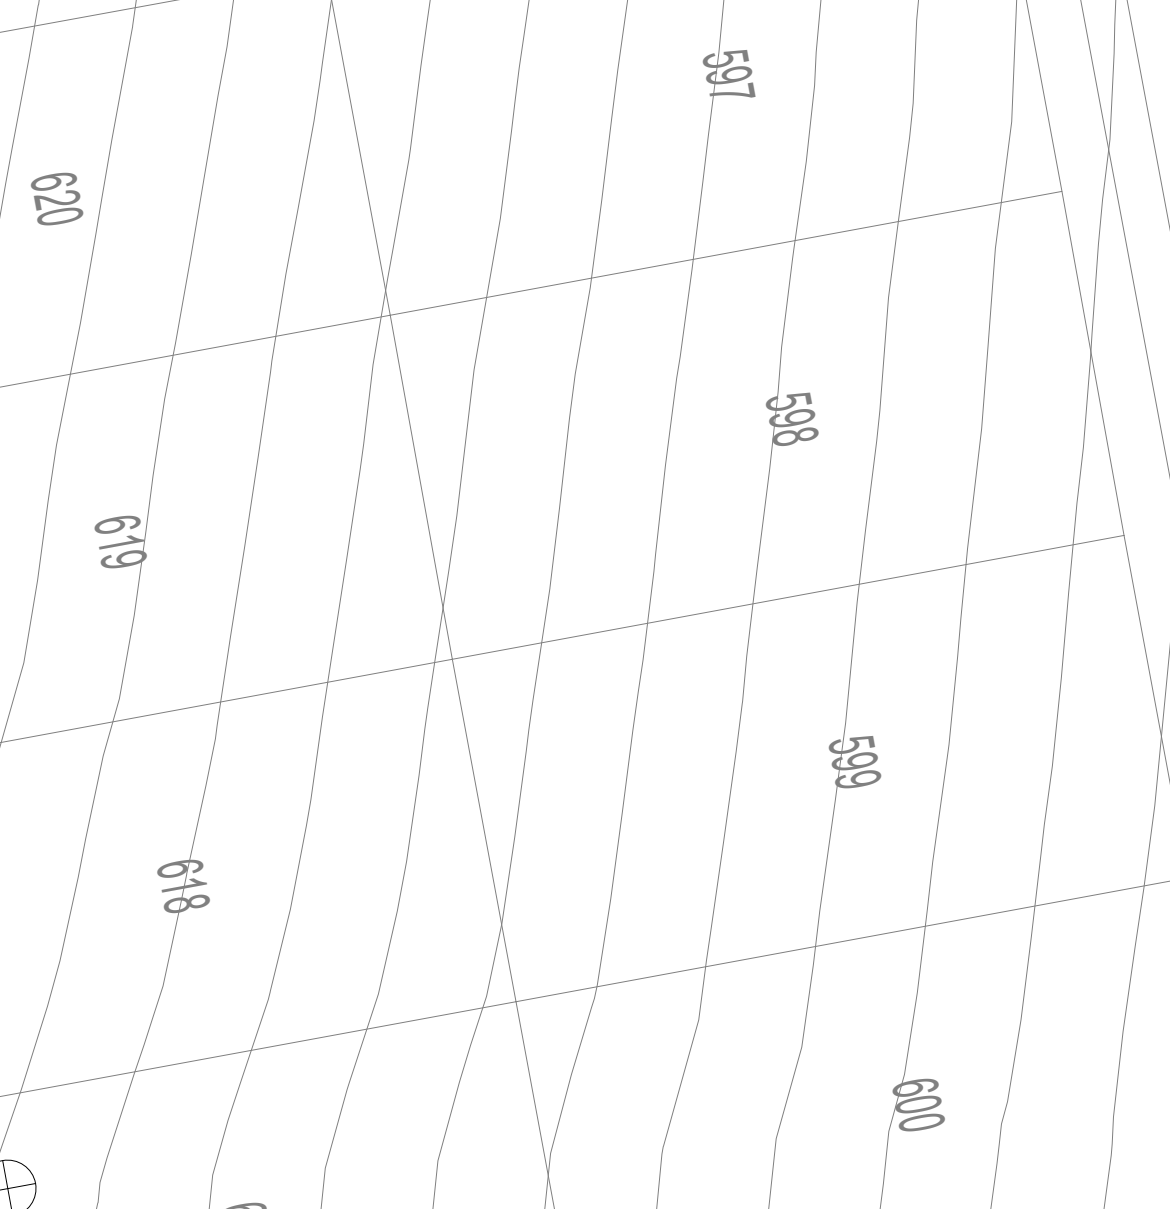


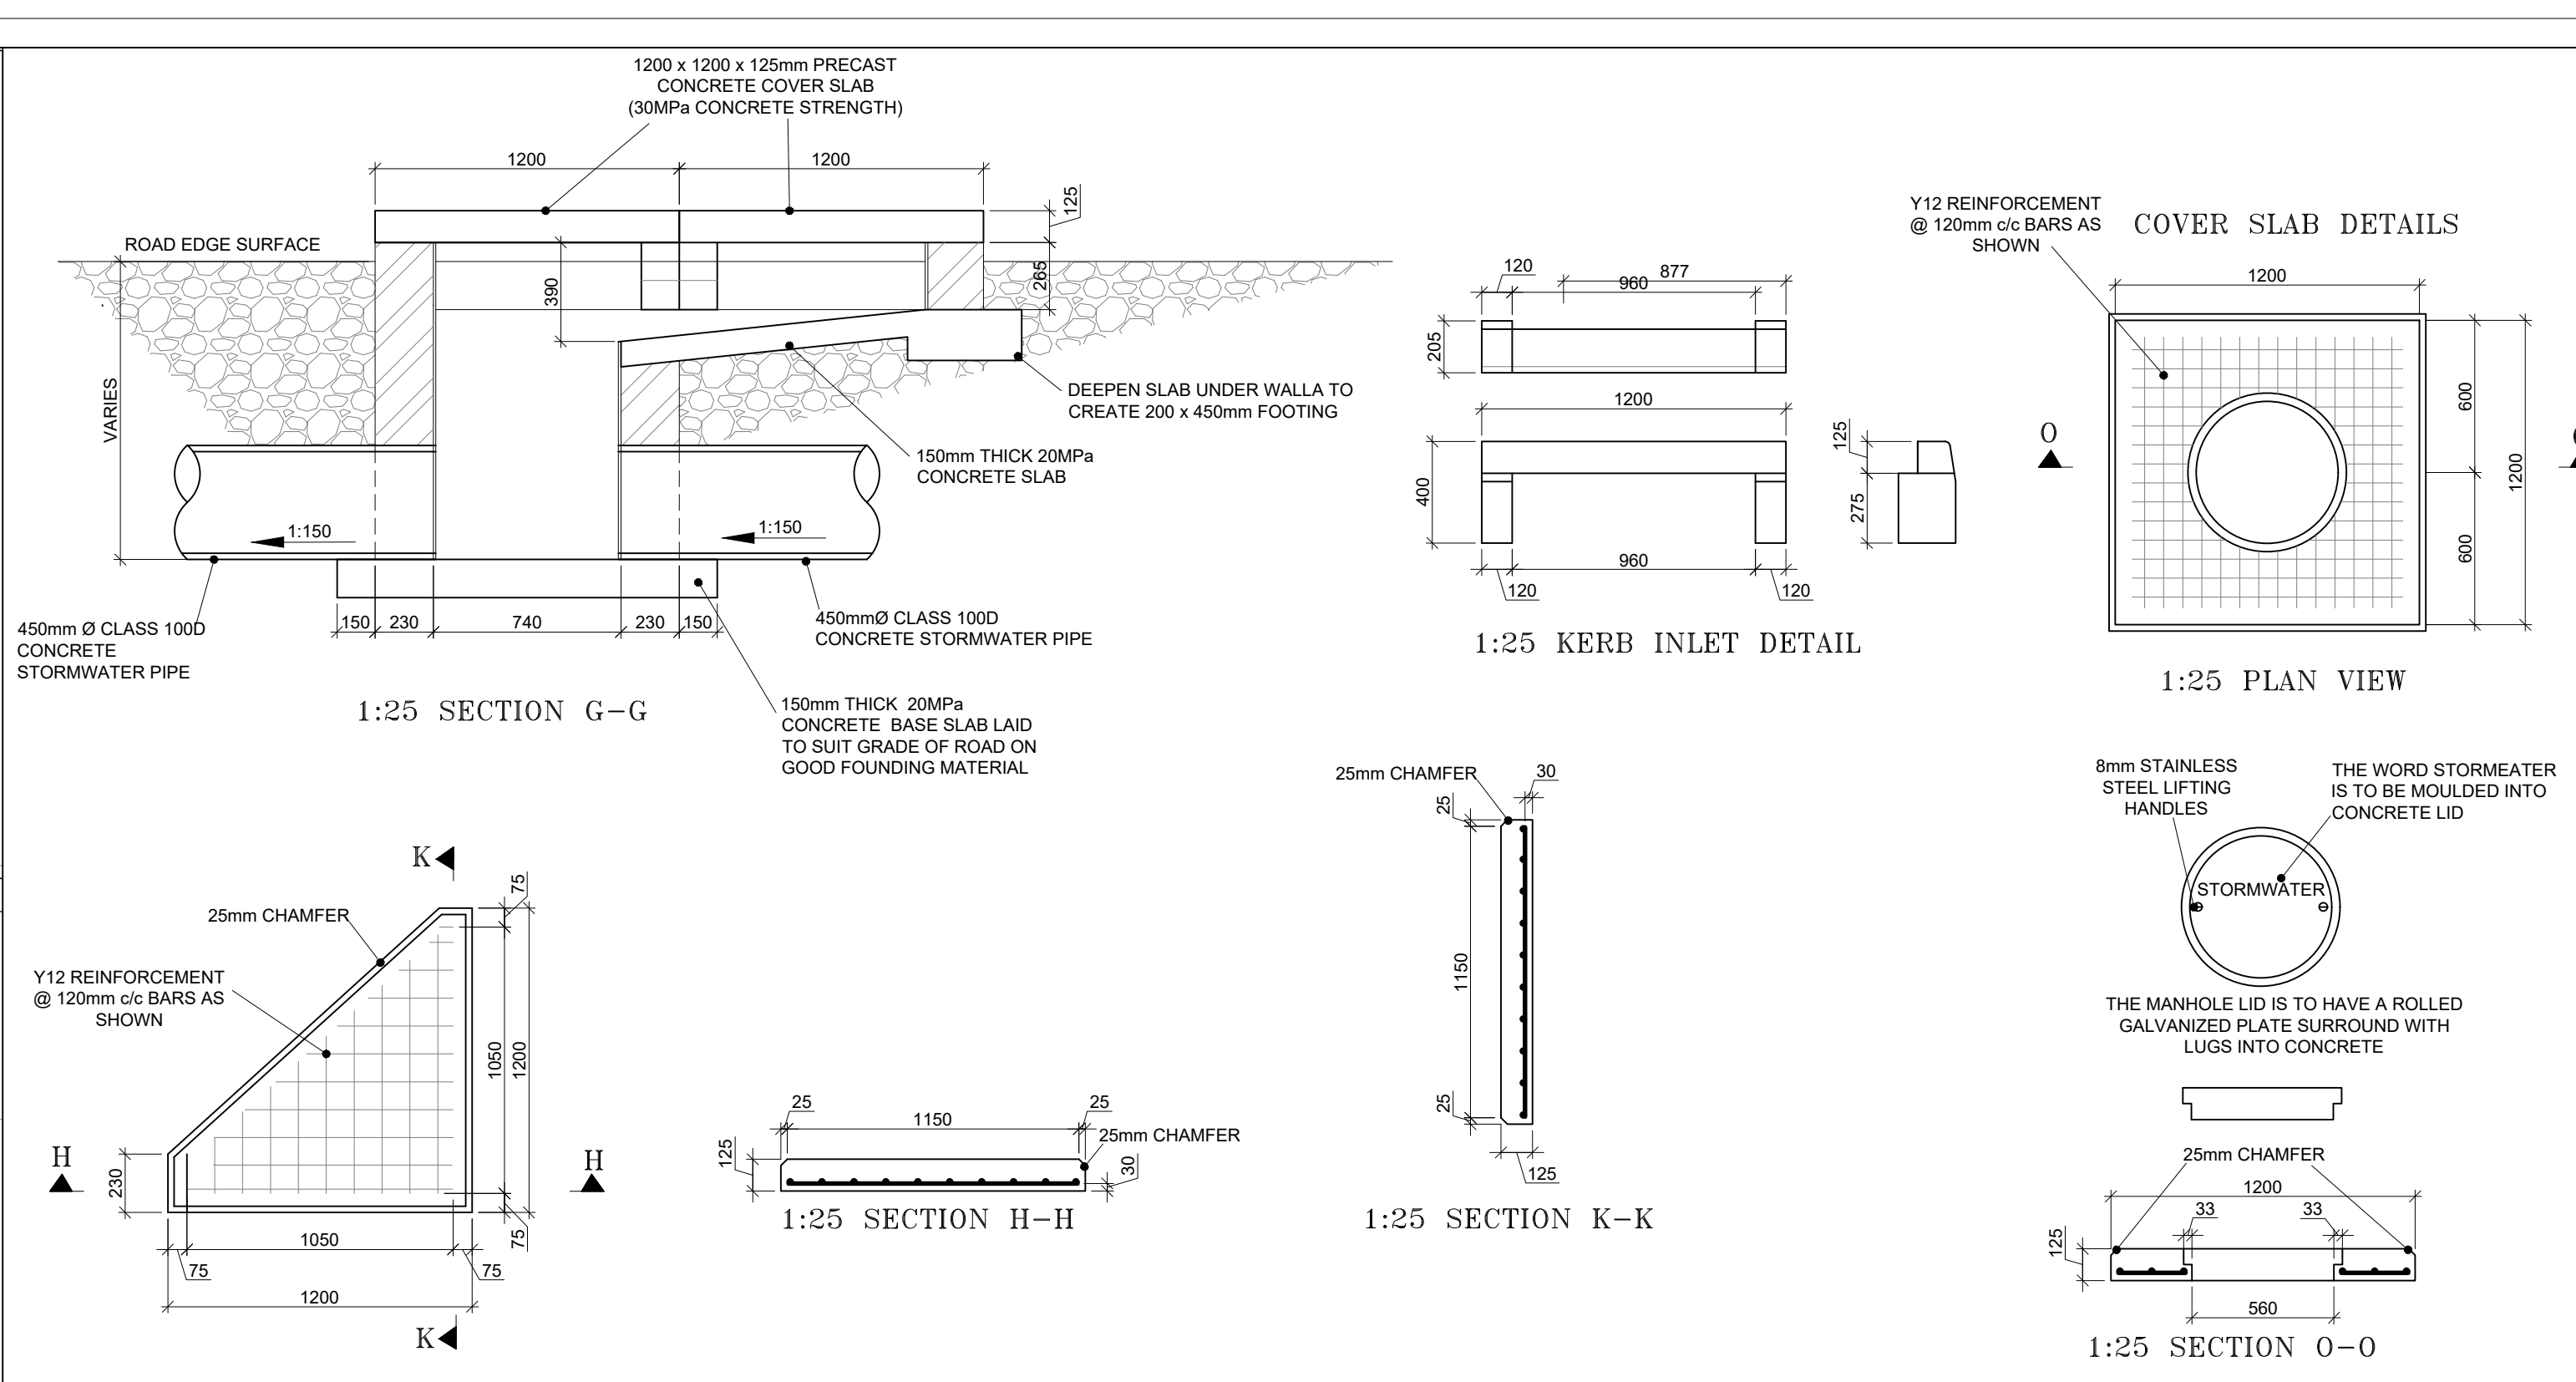

FOR INFORMATION

REV.	DATE	DETAILS	Chd	Appd
A	07-05-2028	INFORMATION		
		REVISIONS		

CLIENT

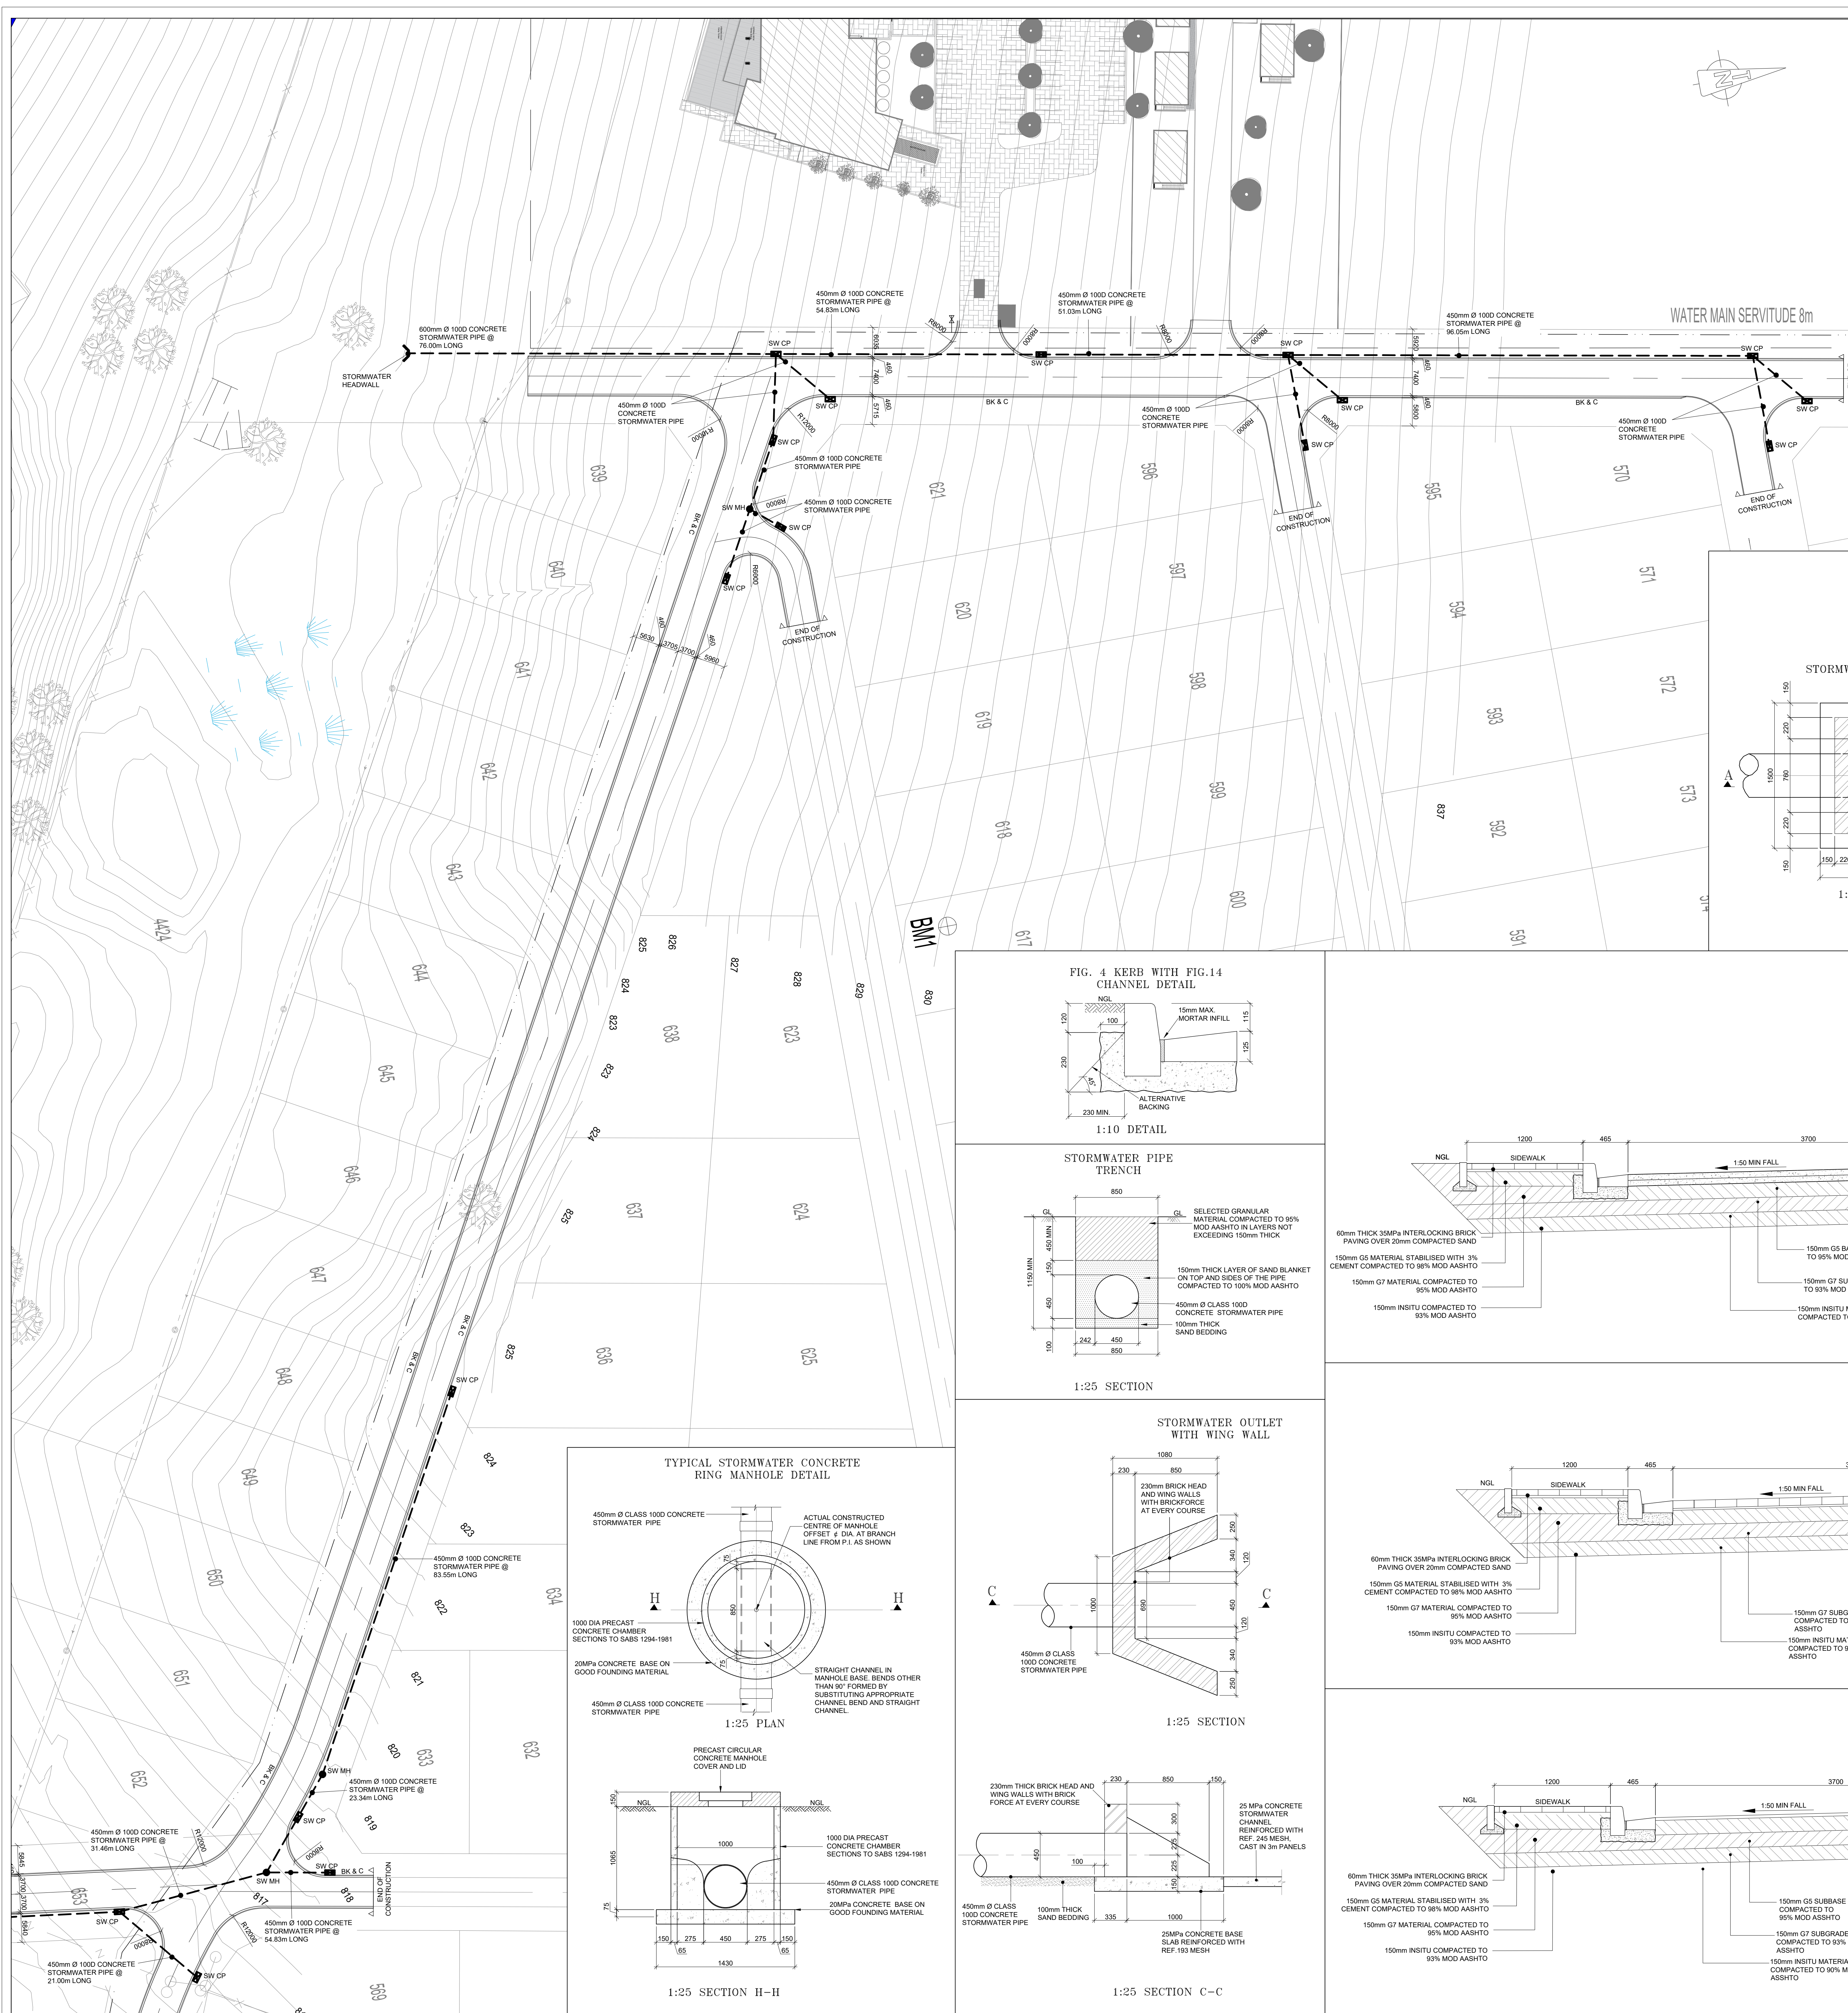

NONXUBA CONSULTING ENGINEERING SERVICES
Civil, Structural & Project Management

No. 20 LATIMER STREET
BERE, EAST LONDON, 5201
Email: nces_ei@nonxubaconsulting.co.za

P.O. BOX 785
EAST LONDON, 5200
TEL: (043) 700 7700
FAX: (043) 742 2891

PROJECT

MBHASHE MUNICIPALITY RECREATION CENTRE

DESCRIPTION

ROAD AND STORMWATER LAYOUT AND DETAILS
Sheet 1 of 2

Drawn NJ	Checked MN	Designed NJ
-------------	---------------	----------------

Scale: 1:500 @ A0 Date: APRIL 2026

Project No: **EL039-2026** Dwg. No: **100** Rev: **A**