



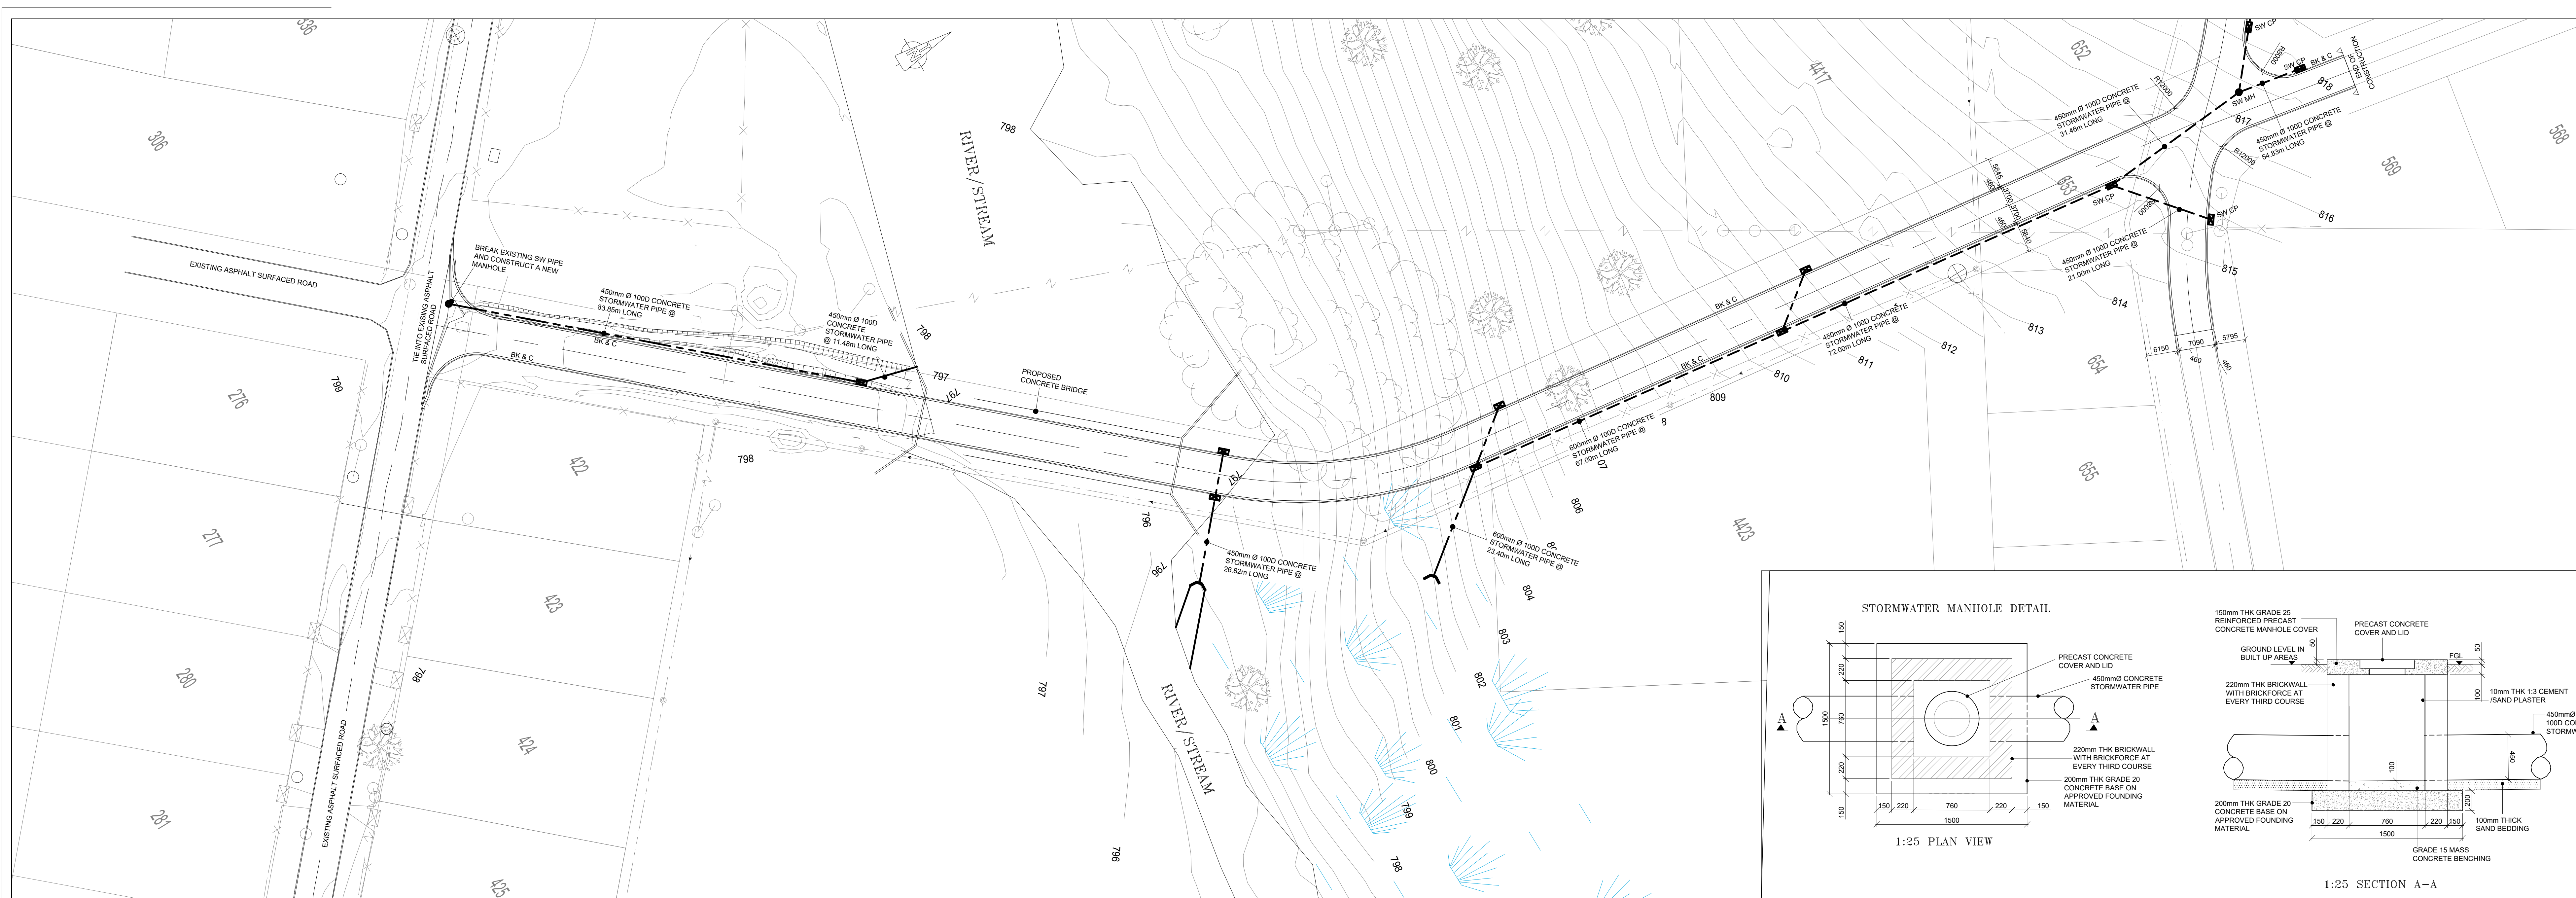


FIG. 4 KERB WITH FIG.14 CHANNEL DETAIL

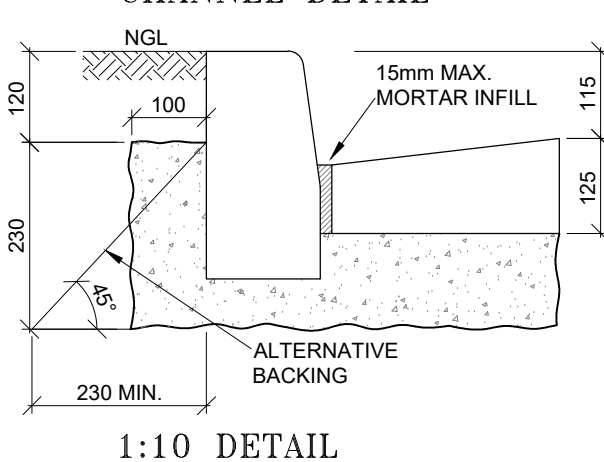


STORMWATER PIPE TRENCH

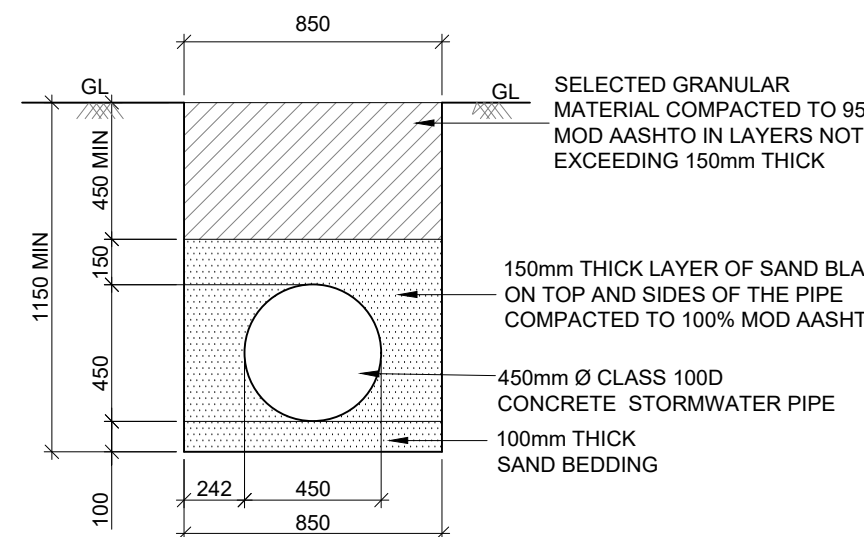


1:25 SECTION

STORMWATER MANHOLE DETAIL

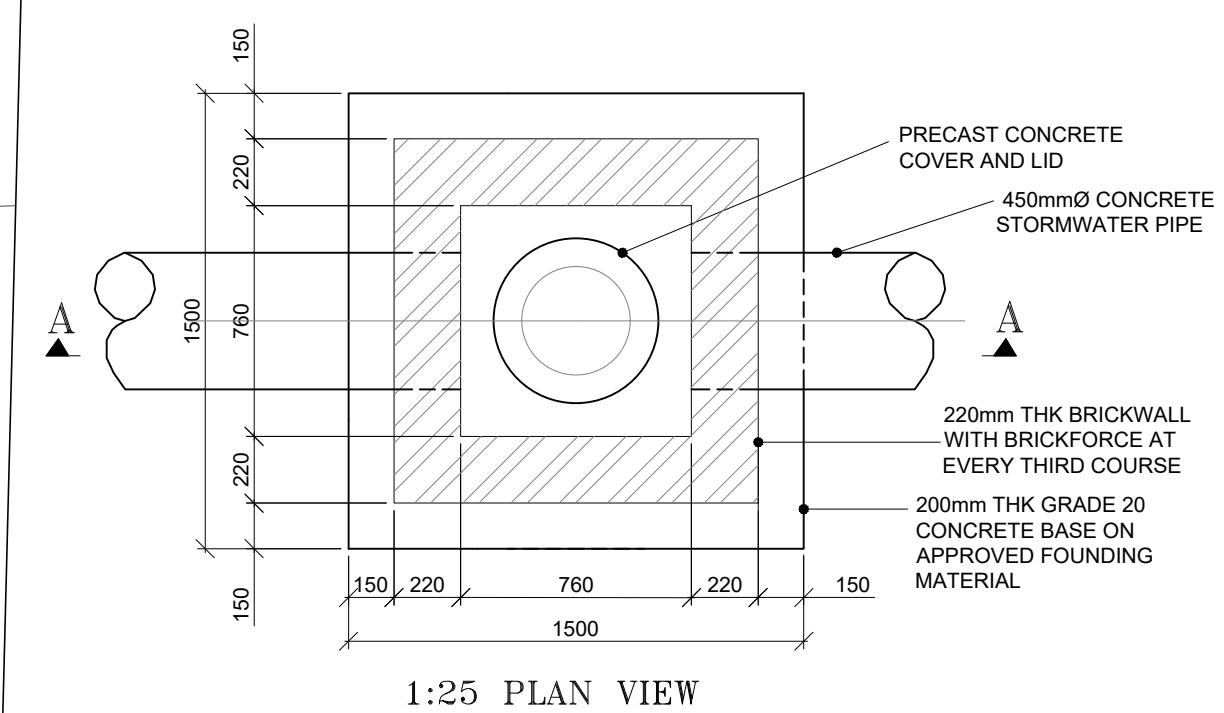


1:25 PLAN VIEW

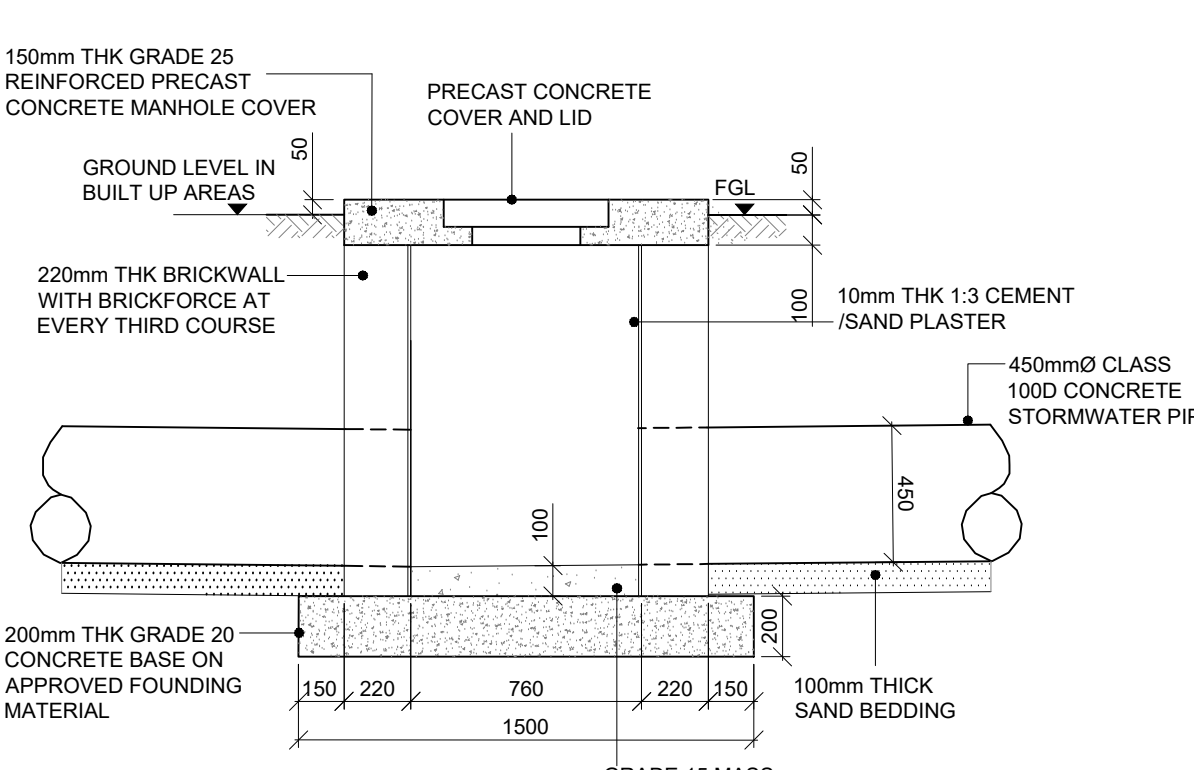


1:25 SECTION A-A

TYPICAL STORMWATER CONCRETE RING MANHOLE DETAIL

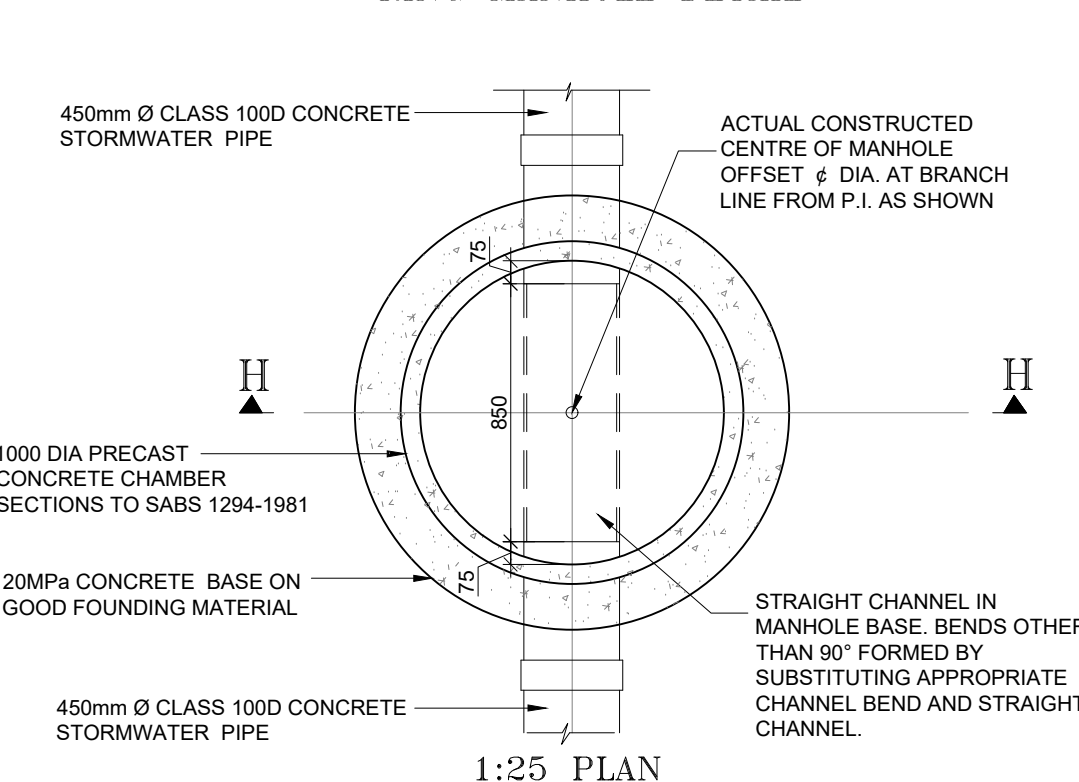


1:25 PLAN

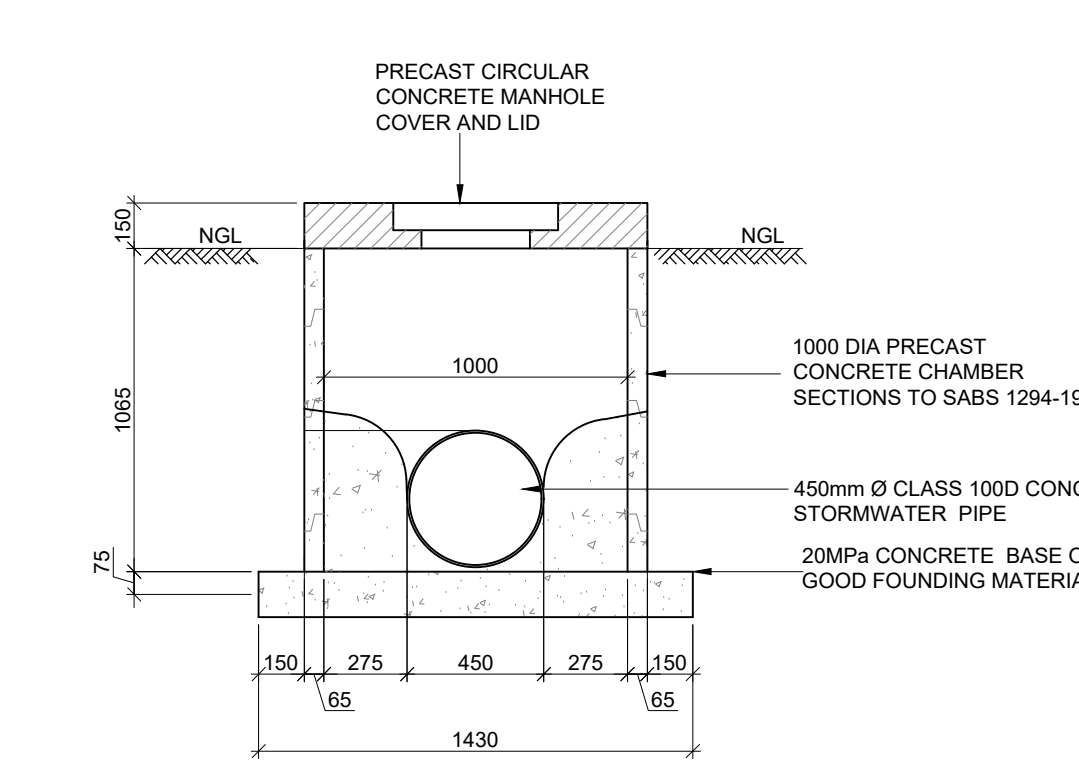


1:25 SECTION H-H

STORMWATER OUTLET WITH WING WALL

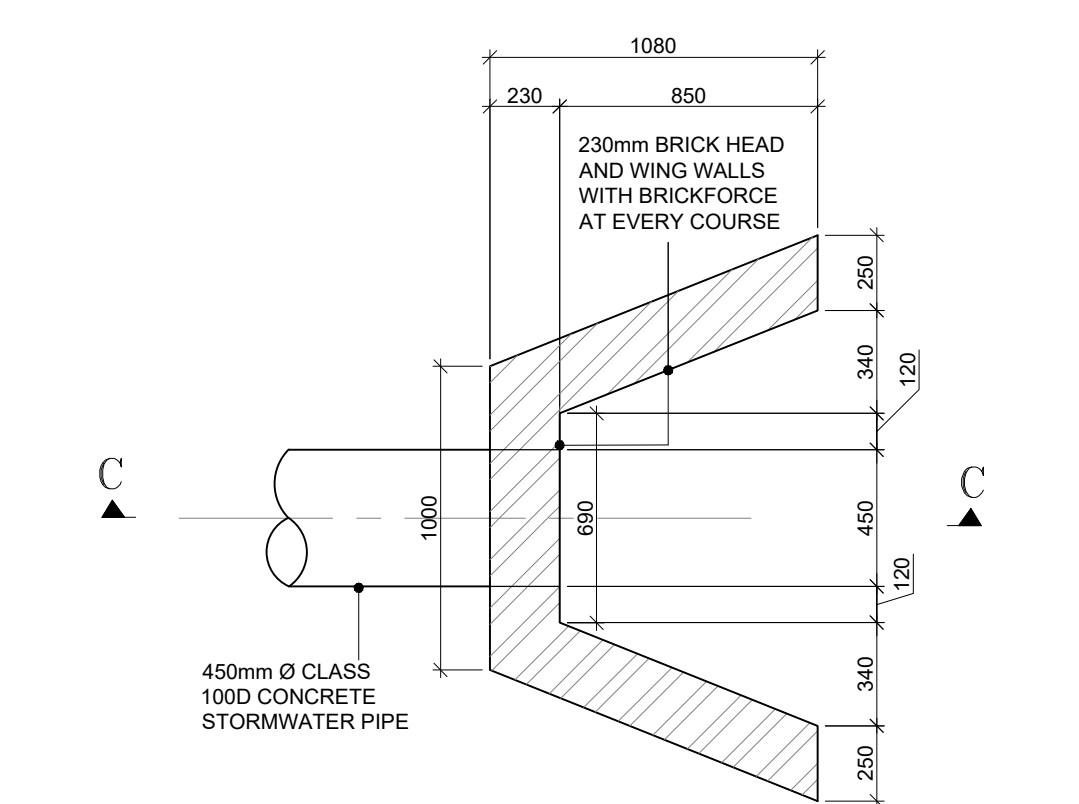


1:25 SECTION

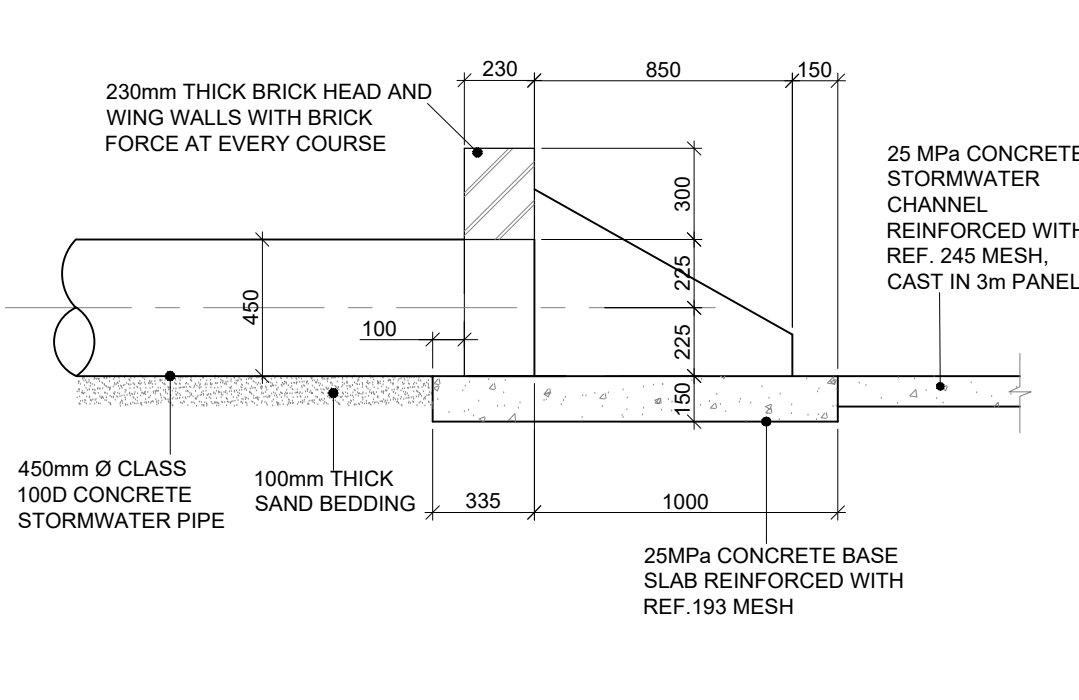


1:25 SECTION C-C

TYPICAL LAYERWORKS UNDER CONCRETE ROAD

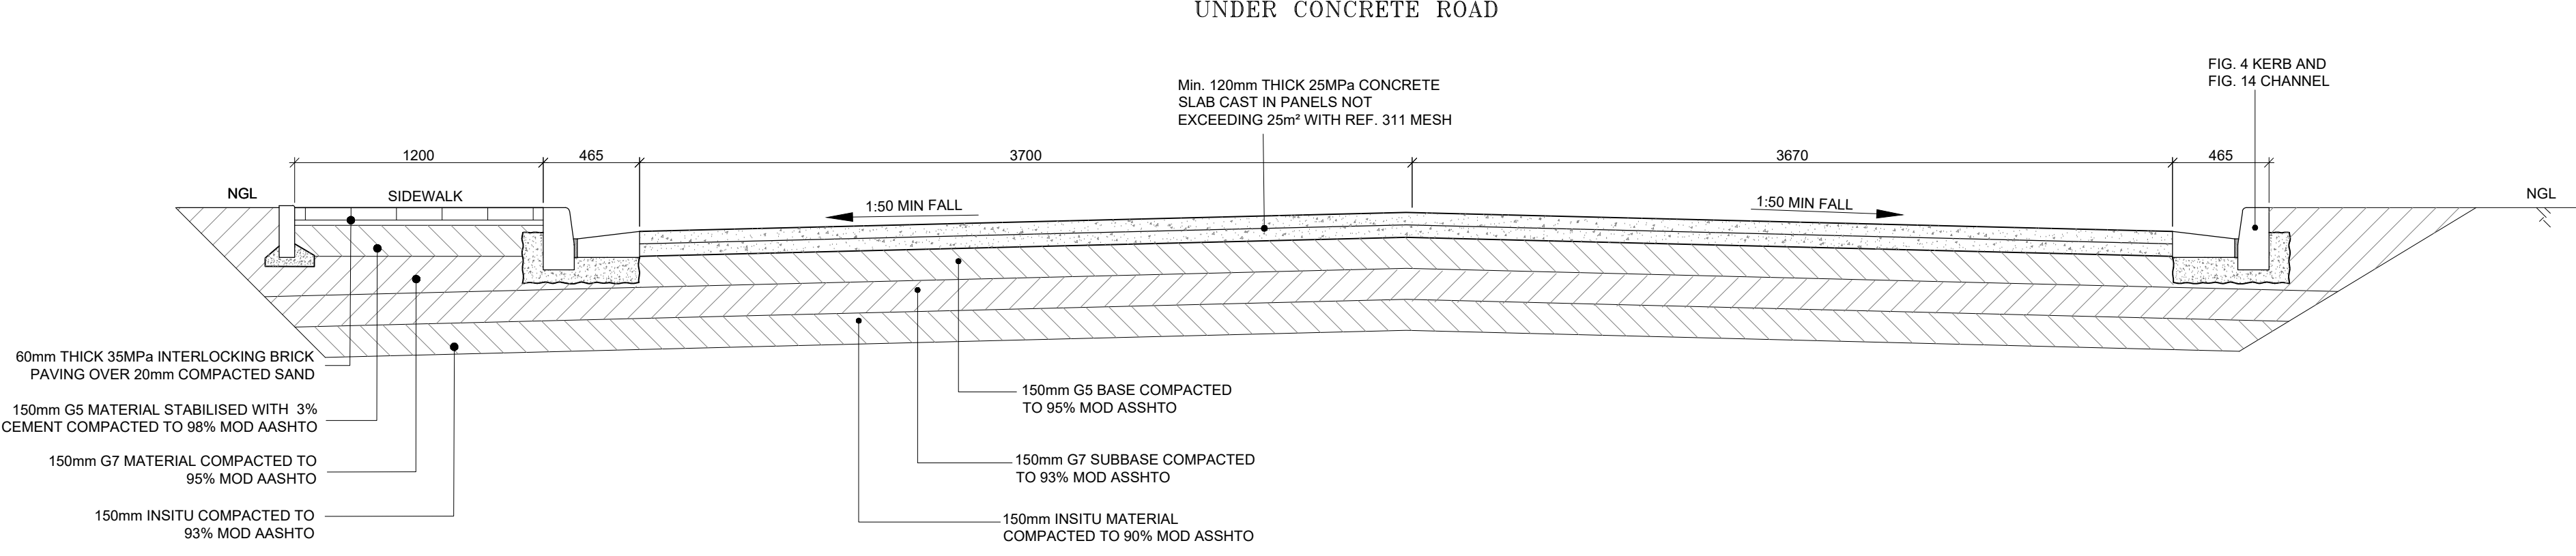


1:25 SECTION

TYPICAL LAYERWORKS UNDER BLOCK PAVED ROAD

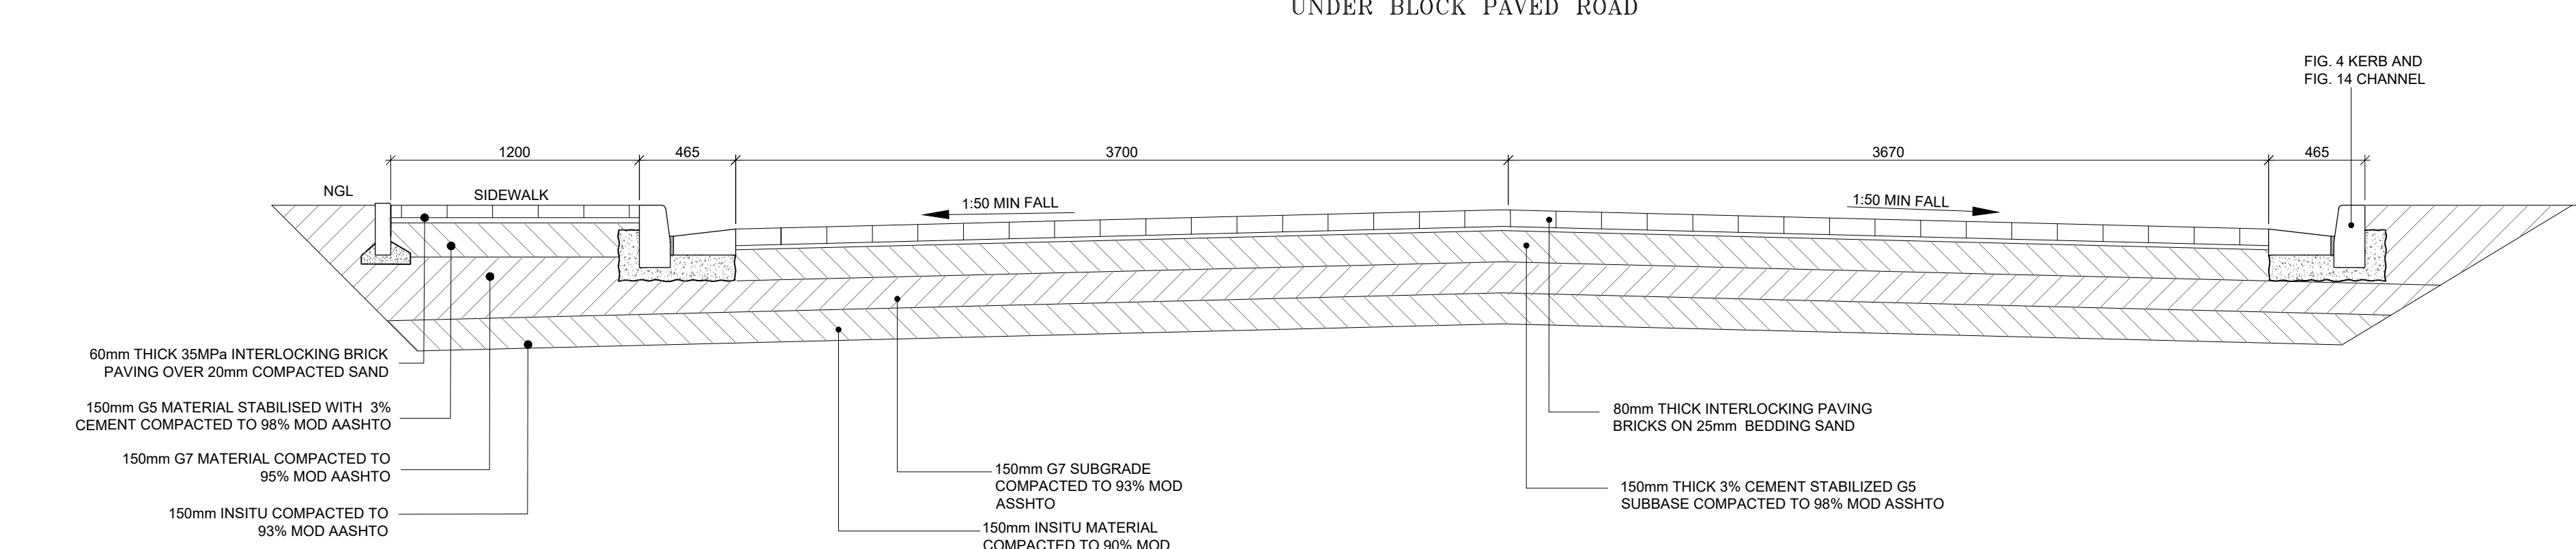


1:25 SECTION


TYPICAL LAYERWORKS UNDER PRE-MIX SURFACED ROAD

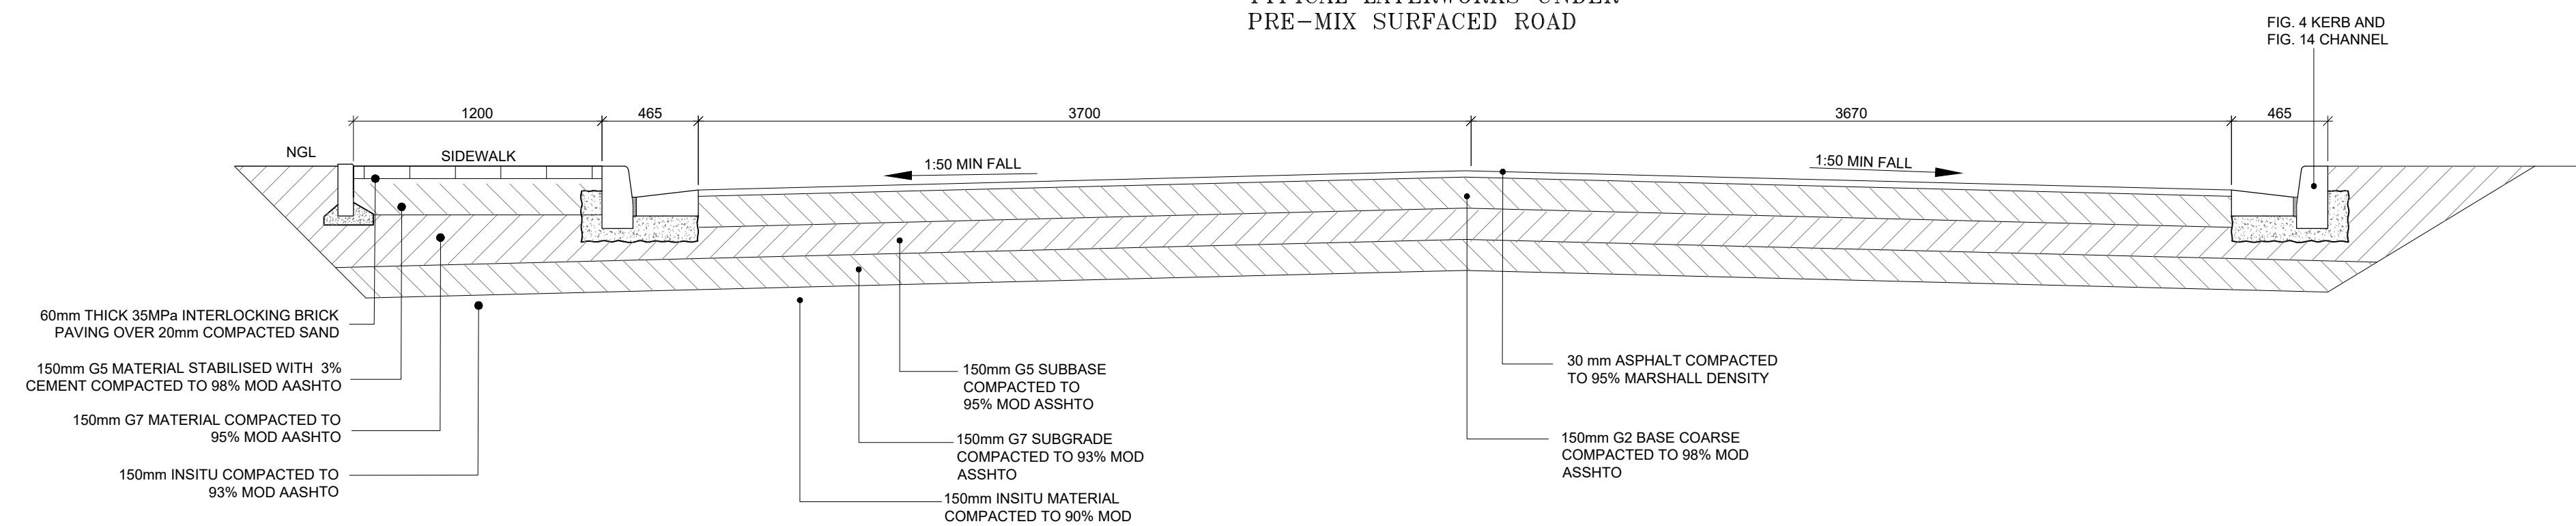


1:25 SECTION

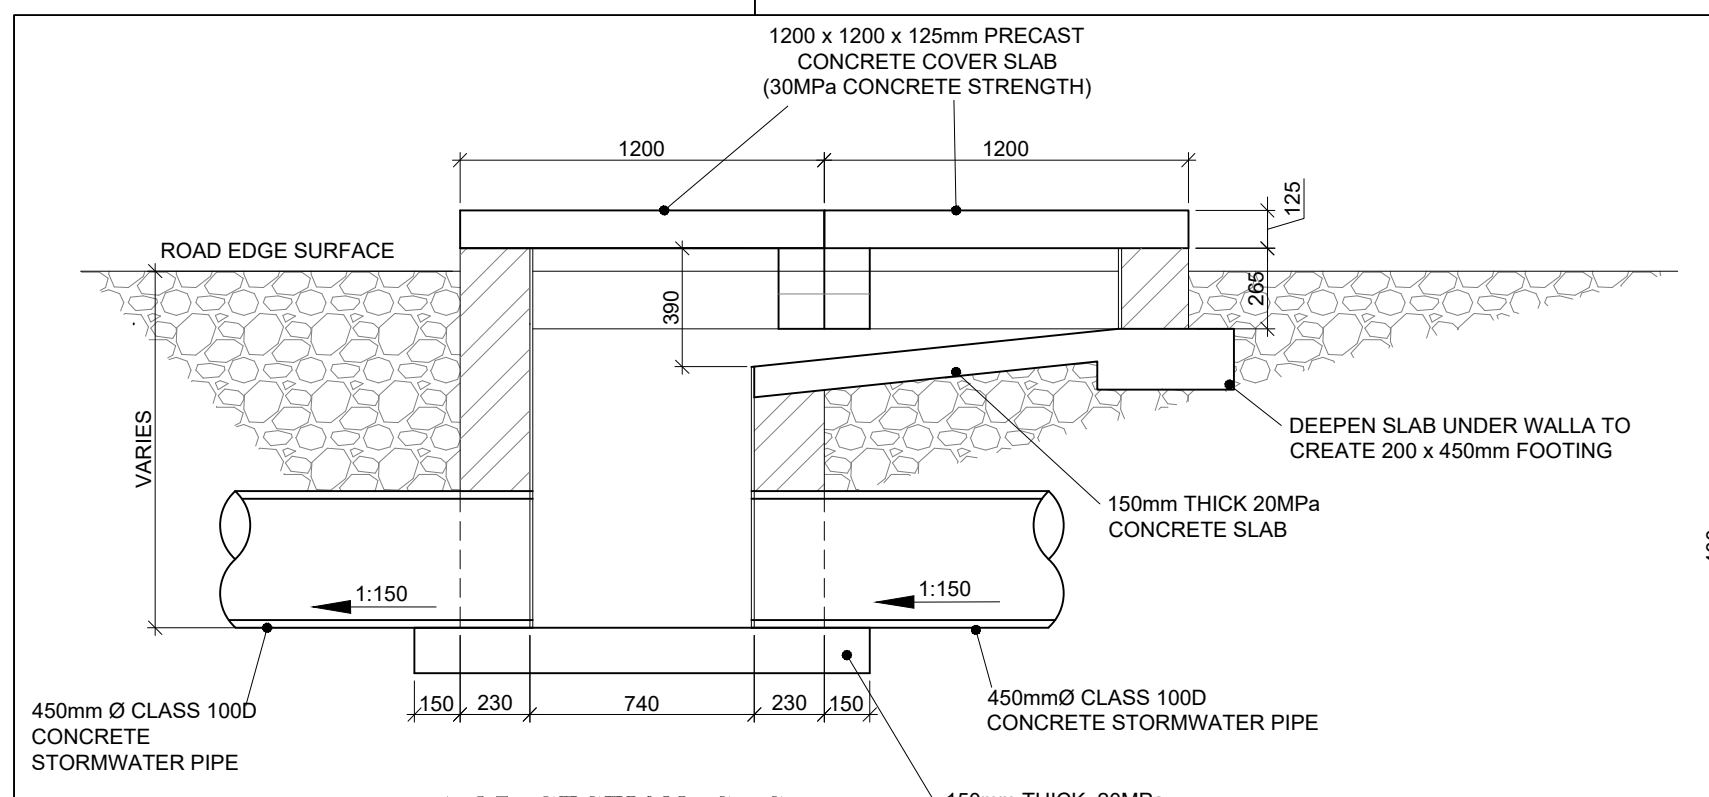


1:25 SECTION G-G

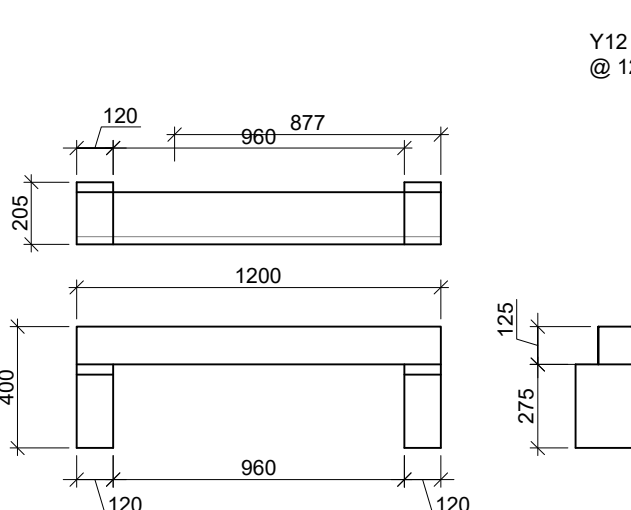

1:25 SECTION K-K

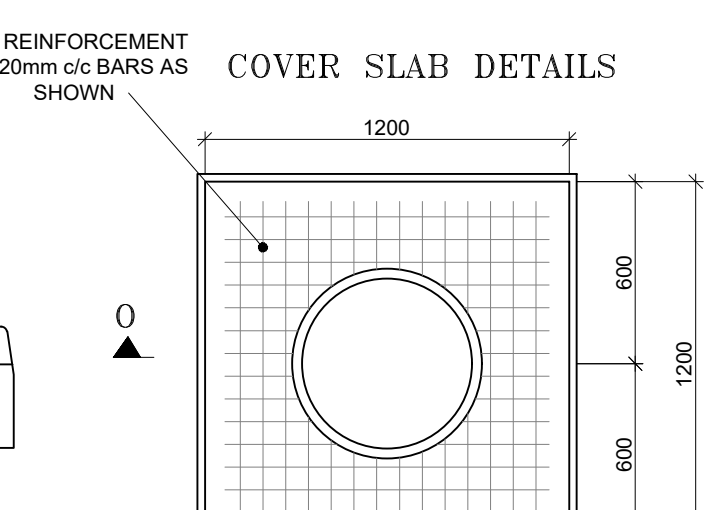

1:25 PLAN VIEW

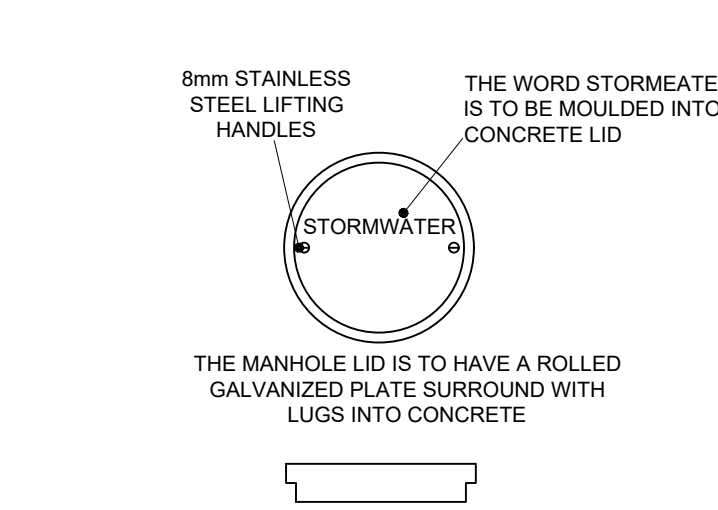


1:25 SECTION O-O

1:25 INLET COVER SLAB DETAIL

FOR INFORMATION

REV.	DATE	DETAILS	Chd	Appd
A	07-05-2026	INFORMATION		
		REVISIONS		

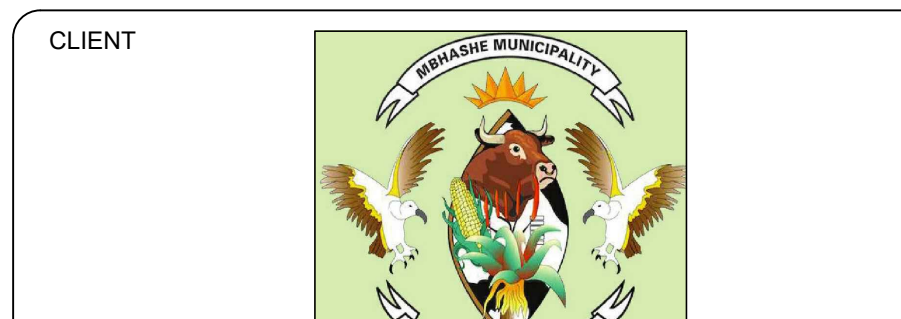

NONXUBA CONSULTING ENGINEERING SERVICES
Civil, Structural & Project Management
No. 20 LATIMER STREET
BEREA EAST LONDON 5201
P.O. BOX 785
EAST LONDON 5200
TEL: (043) 700 7700
FAX: (043) 742 2891
Email: nces_ei@nonxubaconsulting.co.za

PROJECT	MBHASHE MUNICIPALITY RECREATION CENTRE		
DESCRIPTION	ROAD AND STORMWATER LAYOUT AND DETAILS Sheet 2 of 2		
Drawn	Checked	Designed	
NJ	MN	NJ	
Scale	1:500 @ A0		Date
			APRIL 2026
Project No	EL039-2026	Dwg. No	101
		Rev	A