


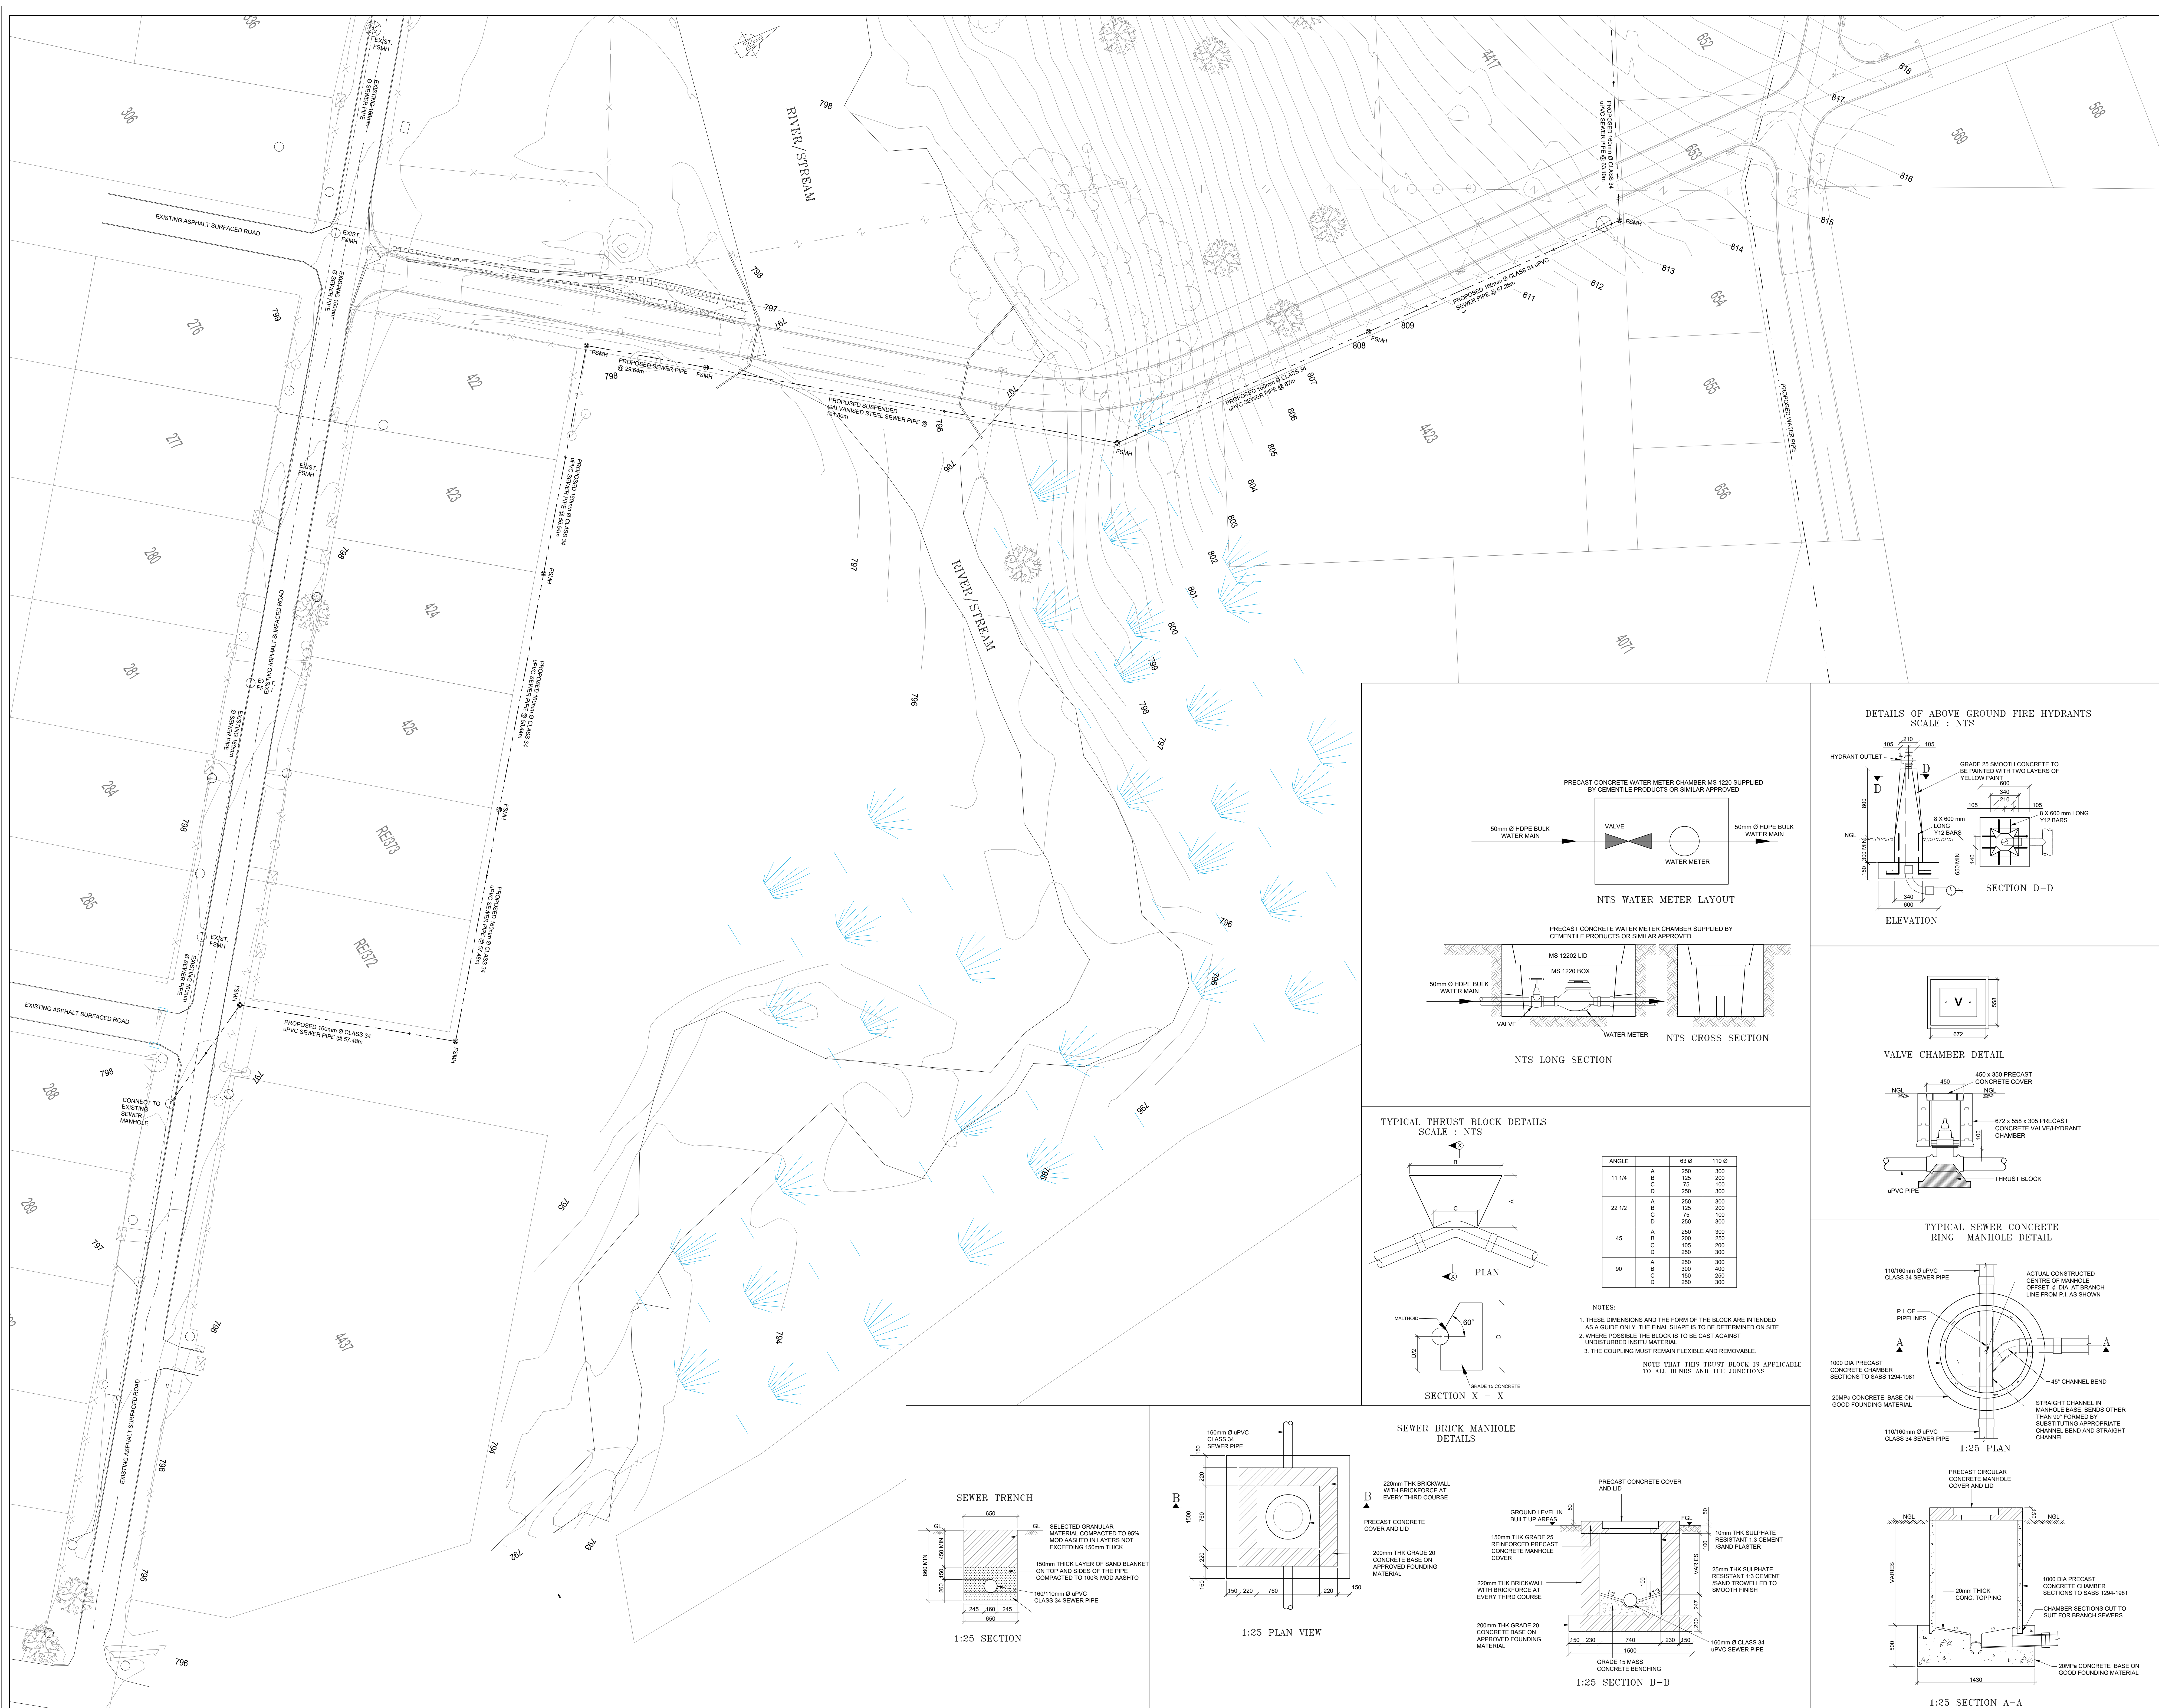

FOR INFORMATION

REV.	DATE	DETAILS	Chd	Appd
A	07-05-2028	INFORMATION		
		REVISIONS		



NONXUBA CONSULTING ENGINEERING SERVICES
Civil, Structural & Project Management

No. 20 LATIMER STREET
BEREA
EAST LONDON
5201

P.O. BOX 785
EAST LONDON, 5200
TEL: (043) 700 7700
FAX: (043) 742 2891

Email : nces_ei@nonxubaconsulting.co.za

PROJECT
**MBHASHE MUNICIPALITY
RECREATION CENTRE**

DESCRIPTION
**WATER AND SEWER
LAYOUT AND DETAILS**
Sheet 1 of 2

Drawn NJ	Checked MN	Designed NJ
Scale 1:500 @ A0	Date APRIL 2026	
Project No EL039-2026	Dwg. No 103	Rev A